


ESCALERA – LÁMINA E-01: REPLANTEO


PLANTA BAJA – REPLANTEO

Escala 1:25 – medidas en m, a caras interiores de muro

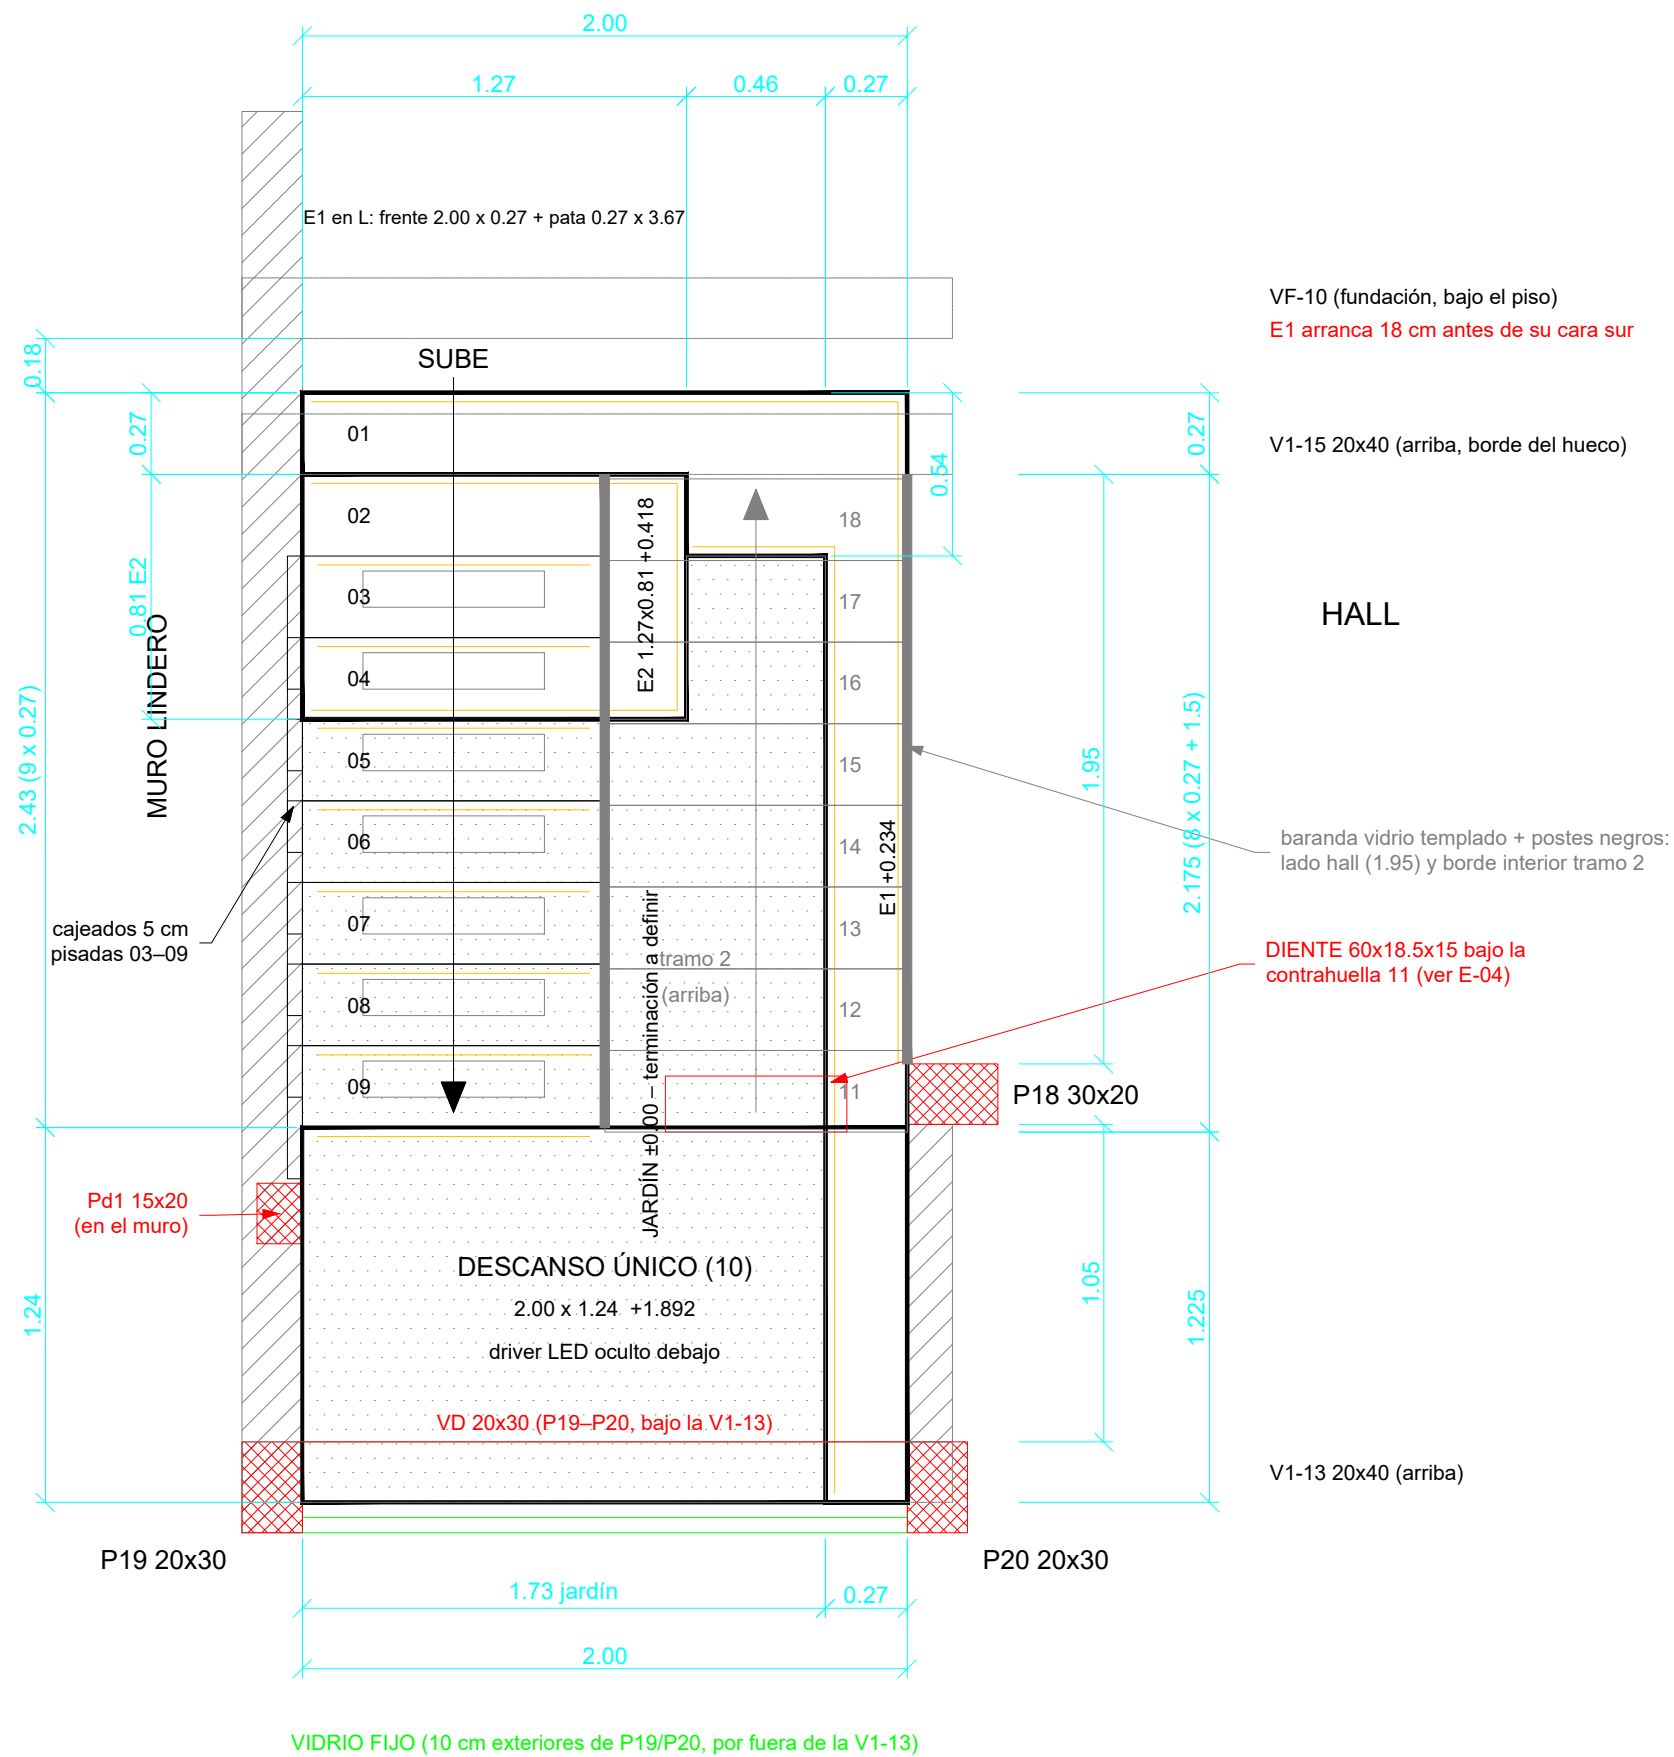

PLANTA ALTA – HUECO Y LLEGADA

Escala 1:25

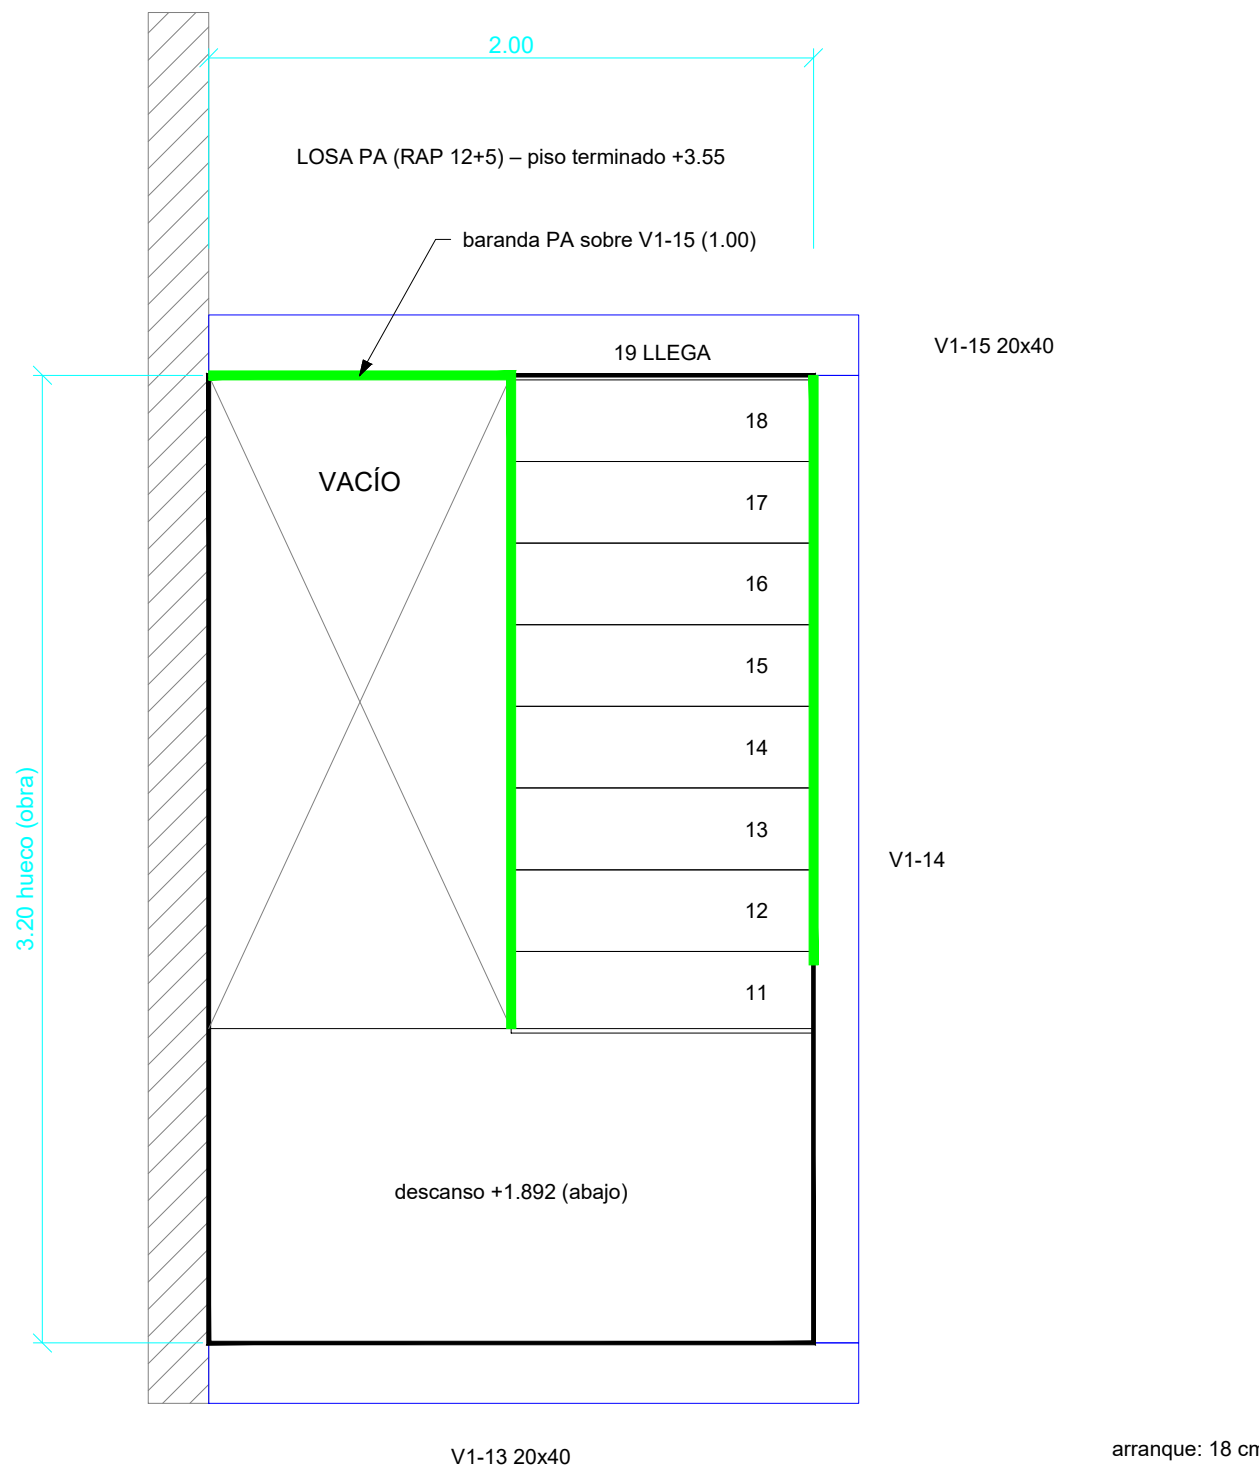


Baranda: vidrio templado laminado 5+5 mm, postes negros c/ 1.00 m máx., altura 0.90 m sobre nariz y 1.00 m en PA. Anclajes de postes: taco químico M10 en el canto de la losa (a 5 cm del borde) – dejar ubicados antes de colocar porcelanato.

Baranda sobre la V1-14 (P18–P20) y sobre la V1-13: A DEFINIR. Se hormigonan ahora: si llevan baranda, dejar los anclajes de los postes antes de hormigonar.

CORTE A-A POR TRAMO 1

Escala 1:25 – niveles desde encadenado terminado ±0.00

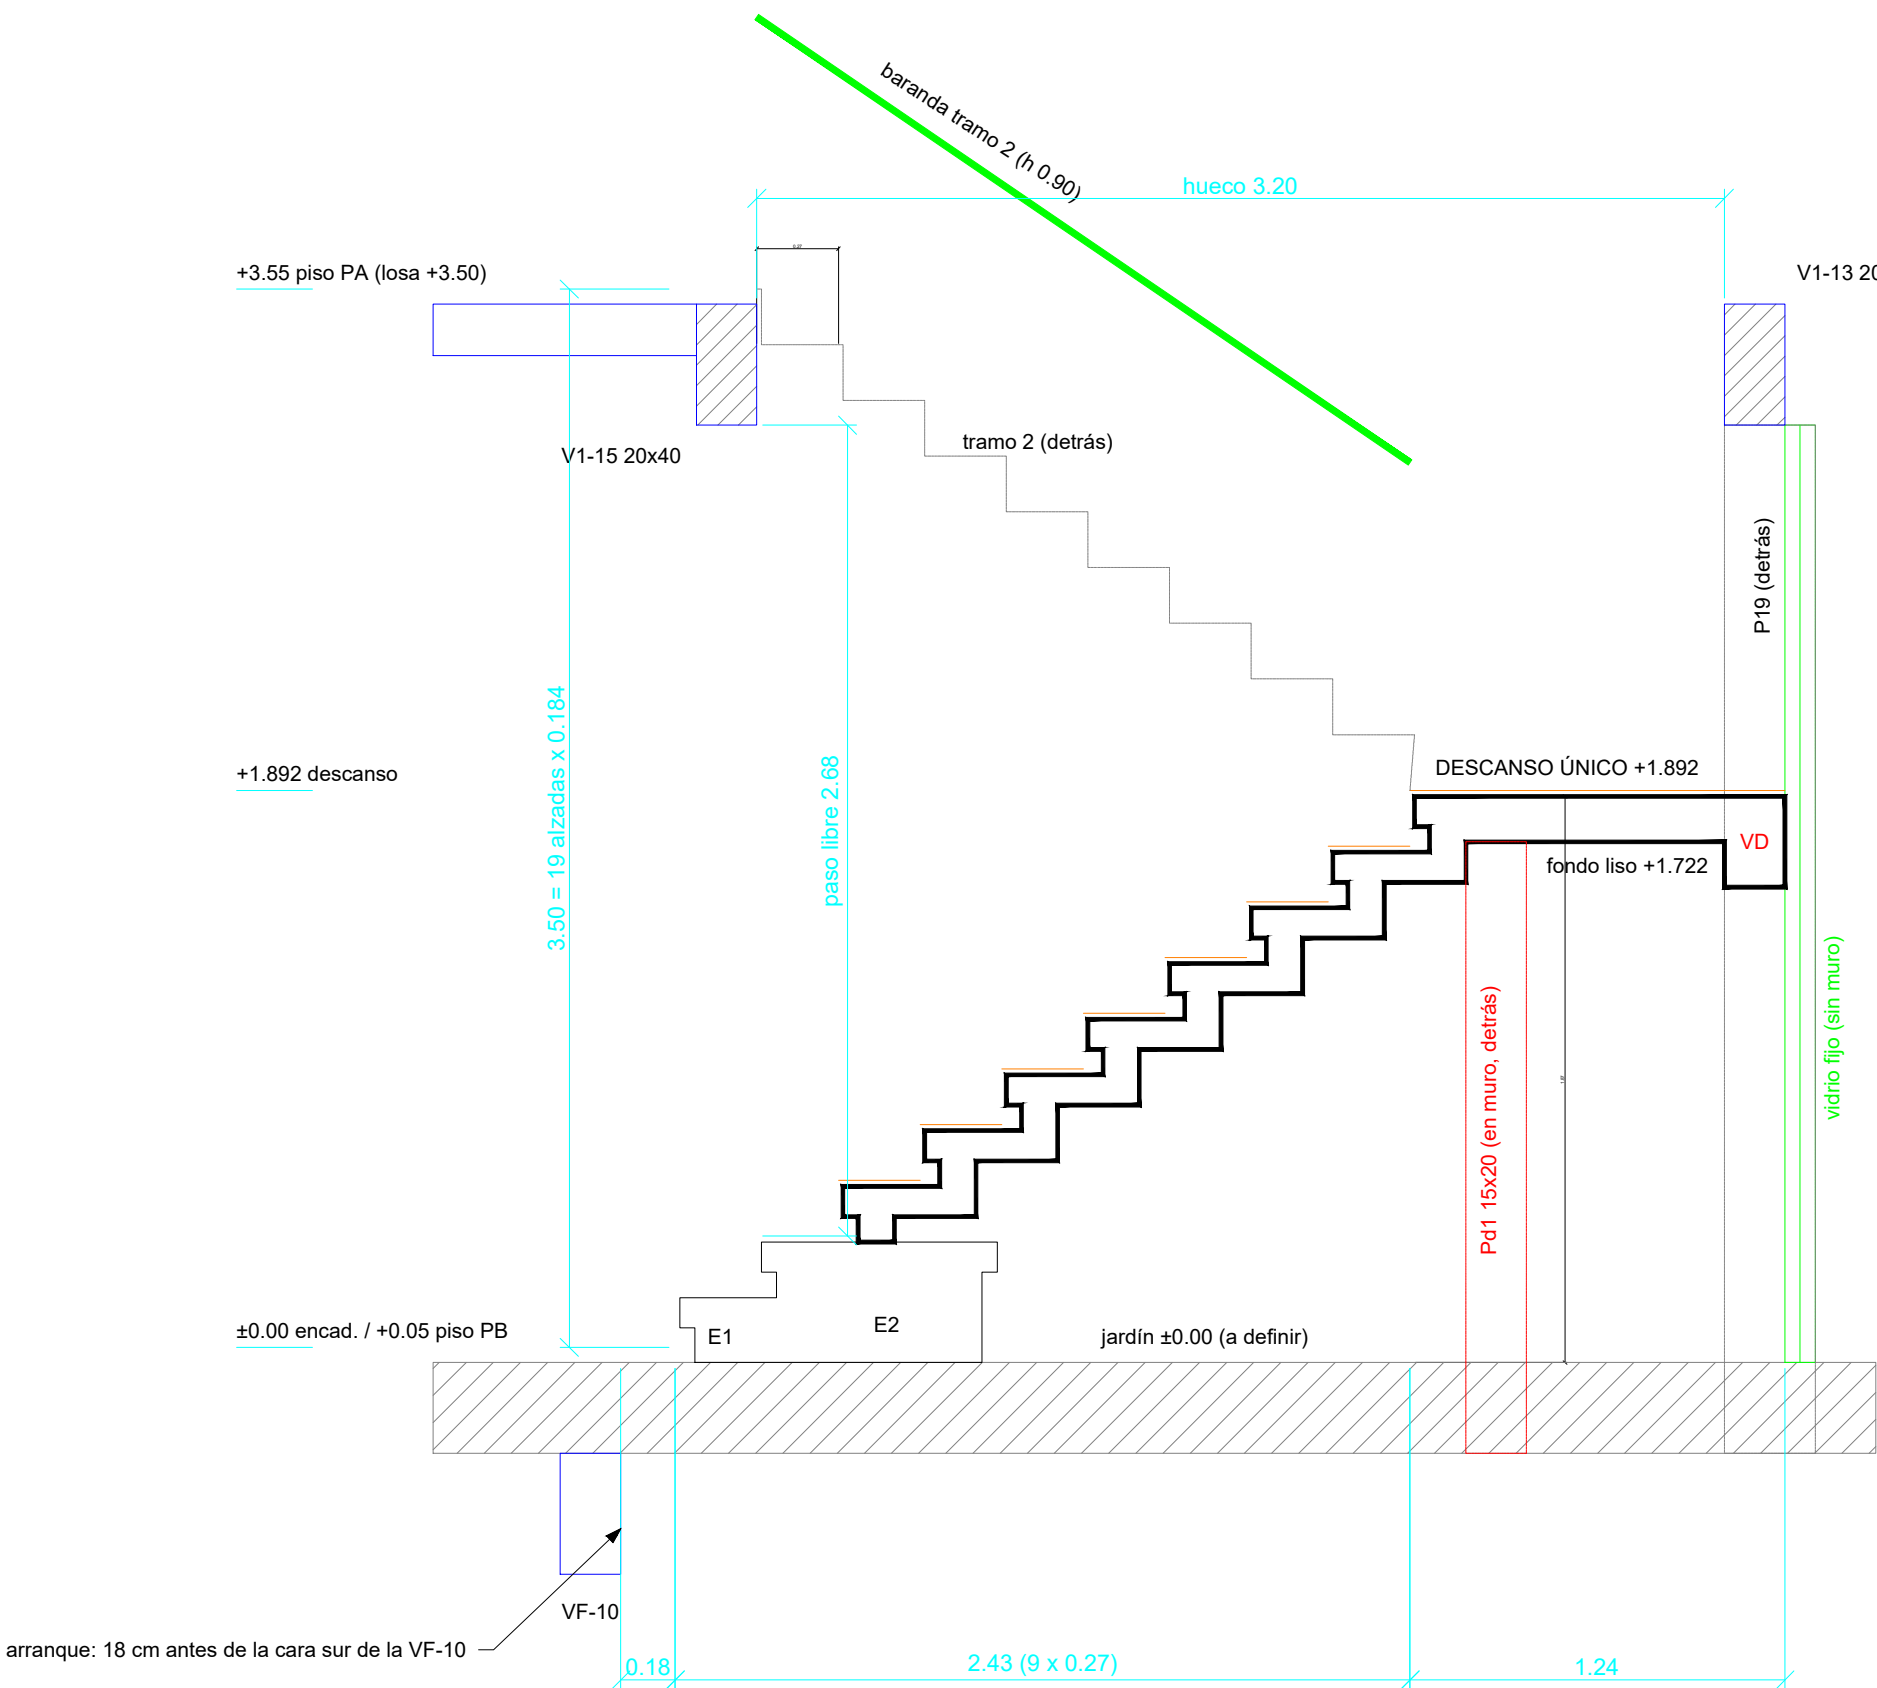

DATOS DE LA ESCALERA

- Altura a salvar: 3.50 m (encadenado a piso terminado PA con 5 cm de piso en cada planta)
- 19 alzadas de 18.4 cm terminadas – huella 27 cm – pisada 10 cm (12 con piso)
- Tramo 1 (lindero): alzadas 1 a 10 – arranca 0.27 al norte de la V1-15 = 18 cm antes de la cara sur de la VF-10
- DESCANSO ÚNICO 2.00 x 1.24 a +1.892 (llega hasta el vidrio sur)
- Tramo 2 (hall): alzadas 11 a 19 – arranca 1.5 cm al sur del frente del descanso: 8 huellas IGUALES de 27 hasta la V1-15
- Contrahuella 11 apoyada en un DIENTE de 60 x 18.5 x 15 bajo la pisada 11 (no se ve terminado)
- ESCALÓN FLOTANTE: contrahuella solo en los 60 cm centrales, 20 cm libres por lado
- E1 en L de 0.27 de ancho: frente 2.00 + pata de 3.67 junto al hall (hasta el vidrio) – E2 1.27 x 0.81 pegado al lindero
- Dentro de la L: JARDÍN en contrapiso ±0.00, terminación a definir (proyecto aparte)
- Paso libre bajo V1-15: 2.68 m
- Ancho de tramos: 1.00 m – nariz 5 cm – porcelanato 11 mm
- P18, P19 y P20 se hacen ahora con la escalera (E-02): P19/P20 20x30 a filo del hueco: 20 cm interiores = VD y descanso bajo la V1-13 20x40; 10 cm exteriores = vidrio fijo
- Descanso de 15 cm con fondo liso (sin viga colgada en el borde)
- E1 y E2 macizos, con nariz 5 cm y LED en todos sus bordes libres (también hacia el jardín) – ver E-07

NIVELES DE HORMIGÓN (sin piso)

Primera alzada en hormigón: 21.4 cm desde el encadenado (E1 +0.214 de H* + 2 cm de piso = +0.234)


Alzadas intermedias: 18.4 cm

Última alzada (llega a PA): 15.4 cm de hormigón + 5 cm de piso PA

Pisada en hormigón = nivel terminado – 2 cm (porcelanato 11 mm + adhesivo 9 mm)

REFERENCIA DE NIVELES

±0.00 = ENCADENADO (cara superior de las vigas de fundación)

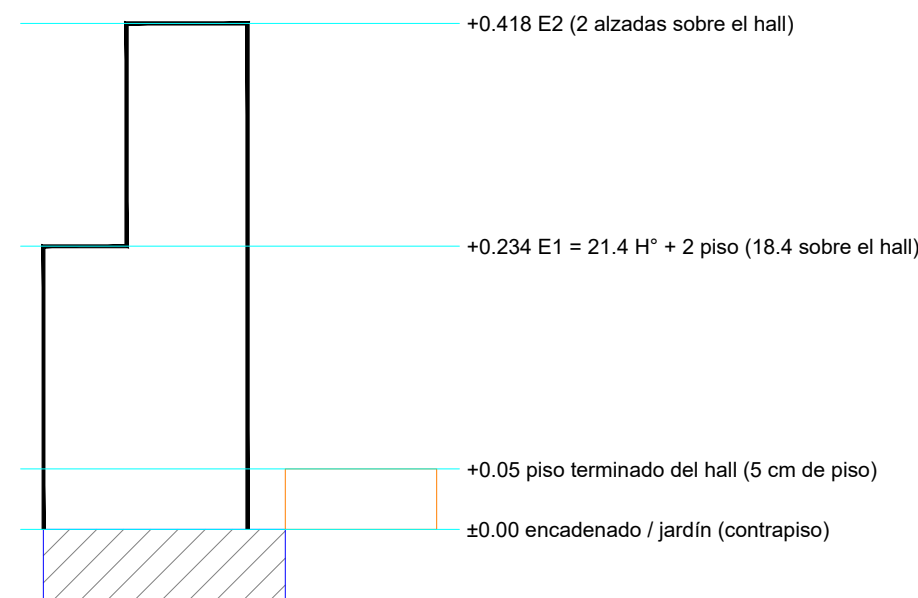

Descanso +1.892 - piso PA +3.55 (losa +3.50)

cada alzada: 18.4 cm terminada

SECUENCIA DE OBRA (orden general de toda la escalera)

1. Pilares P18, P19 y P20 (nuevos, E-02): armar empalmando con los pelos de sus bases (≥ 50 cm Ø12 / 40 cm Ø10) y hormigonar hasta +1.572 (junta 1). Dejar sus barras para arriba.
 2. Pd1 15x20 (E-03): abrir el muro lindero, anclar 4Ø10 con epoxi a su VF y hormigonar hasta +1.572. Perforar la V1-15 para las horquillas pos. 7, evitando sus hierros.
 3. Cajeados de 5 cm en el lindero para las pisadas 03–09 (5x12x45) y canaleta de 15 x 30 en cada muro para VL1 y VL2 (quedan enteras dentro del muro).
 4. E1 en L y E2 macizos sobre el contrapiso, sin relleno, con mezcla A, sus narices, el enlace E1–E2 y los pelos pos. 3 (E-07). Jardín en contrapiso ±0.00: dejar caño 3/4" y caja para luces.
 5. Encofrado en una sola etapa: VD, VL1 y VL2 (fondo +1.572), descanso con fondo liso (+1.722) y tramos. Dejar LIBRES los 10 cm de P19/P20 que salen por fuera de la V1-13 (vidrio). Caño 3/4" dentro de cada contrahuella.
 6. Armar: pilares y nudos (E-02), vigas (E-03), descanso (E-04) y cada escalón (E-06; pisada 18 con 8 horquillas Ø10 con epoxi en la V1-15, sin E-P). Separadores de 2 cm.
 7. Hormigonar TODO JUNTO, de abajo hacia arriba, con mezcla A (gravilla 6-12): vigas, nudos de los pilares hasta +1.872 (junta 2), cabeza del Pd1, descanso y tramos.
 8. OBLIGATORIO: el tramo 2 se hormigona junto con el descanso y anclado a la V1-15 (controla la flecha). Vibrar o varillar cada escalón.
 9. Pilares de +1.872 a +3.10 (junta 3).
 10. V1-13 y V1-14 con el nudo de arriba (+3.10 a +3.50), armado según el ingeniero.
- En cada junta: picar, limpiar y mojar antes de seguir. Curado húmedo 7 días. Desencofrar costados a los 3 días; fondos y puntales a los 21 días.

NOTAS PARA EL ALBAÑIL

1. Marcar en la pared lindero el perfil de todos los escalones con hilo y nivel ANTES de encofrar.
2. Todas las alzadas deben ser iguales (tolerancia ±3 mm).
3. LED: perfil de aplicar 16x7 mm pegado bajo cada nariz, contra la contrahuella (sin ranura). También en E1, E2 y el descanso.
4. Dejar el caño corrugado 3/4" de cada escalón unido, bajando hasta la caja del driver bajo el descanso.
5. Prever cajas de paso y la caja del driver ventilada y accesible.
6. Dejar los tacos de los postes de baranda antes del porcelanato.
7. Curado: mojar 7 días. Desencofrar costados a los 3 días y fondos a los 21 días.
8. El porcelanato de la nariz se corta a 45° o con perfil de terminación.
9. Última alzada (llegada a PA): el borde es la V1-15; LED en perfil de aplicar igual que el resto.
10. Vidrio sur: va en los 10 cm de P19 y P20 que sobresalen por fuera de la V1-13. Dejarlos LIBRES (sin hormigón ni ladrillo).
11. Replanteo del arranque: el frente de E1 queda a 0.27 de la cara de la V1-15 (18 cm antes de la cara sur de la VF-10).
12. Escalón flotante: encofrar la contrahuella solo en los 60 cm centrales; cantos laterales de la pisada con porcelanato.
13. EMPOTRAMIENTO: pisadas 03 a 09 entran 5 cm en el lindero (cajeado de 5 x 12 x 45 cm por pisada, NO regata corrida).
14. VL1 y VL2 (15x30) y Pd1 van ENTEROS dentro de su muro (canaleta de 15 x 30 para las VL); no asoman. Pd1 queda debajo de las 3Ø16.
15. E1 y E2 van directo sobre el contrapiso (suelo compactado): sin zapata ni pilotes. Sondear igual al romper: si aparece relleno flojo, avisar.

REFERENCIAS

qué es cada capa (color) del dibujo – vale para TODAS las láminas E-01 a E-08

- E-ESCALERA: contorno de hormigón nuevo
- E-HORMIGON: rayado (puntitos) del hormigón
- E-ACHURA: RAYADO de muros, rellenos y contrapiso cortados (no es un elemento)
- E-EST-EXIST: estructura existente (V1-15, VF y bases)
- E-EST-NUOVA: estructura nueva: VD, VL1, VL2, Pd1 y pilares P18, P19, P20
- E-HIERRO: ROJO: estribos, E-P, E-C, U y horquillas (barras dobladas que abrazan)
- E-HIERRO-REP: AZUL: barras rectas o con gancho en las puntas (esquinas, mallas, barras de vigas, pelos)
- E-HIERRO-U: VIOLETA: estribos laterales cerrados de las pisadas (pos. 38/39/39b)
- E-HIERRO-PIL: MARRÓN: barras de los pilares P18, P19 y P20
- E-HIERRO-EX: GRIS: barras existentes (pelos de las bases, V1-15)
- E-LED: perfil LED y su luz
- E-PORCEL: porcelanato + adhesivo
- E-BARANDA: vidrio fijo y baranda
- E-OCULTO: elementos ocultos o detrás (trazos)
- E-COTAS: cotas
- E-FIGURA: personas y pie de referencia

IMPORTANTE: predimensionado. Verificar medidas en obra antes de encofrar. La estructura debe ser revisada y firmada por el profesional responsable de la obra.

OBRA: VIVIENDA RODRIGO RUIZ DÍAZ
ESCALERA SEMI CASCADA EN U – REPLANTEO Y SECUENCIA DE OBRA
Escala 1:25 (indicada en cada detalle) – Medidas en m (detalles en cm)
Lámina E-01 Fecha: 01/10/2026 (v21) H21 – ADN 500