


ESCALERA – LÁMINA E-05: TRAMOS 1 Y 2 – ARMADO


DETALLE DE ARMADO – TRAMO 1

Escala 1:10 – cotas en cm – el tramo 2 se arma igual, SALVO la contrahuella 11 (apoya en el DIENTE, ver E-04) y la pisada 18 (horquillas, ver LLEGADA)

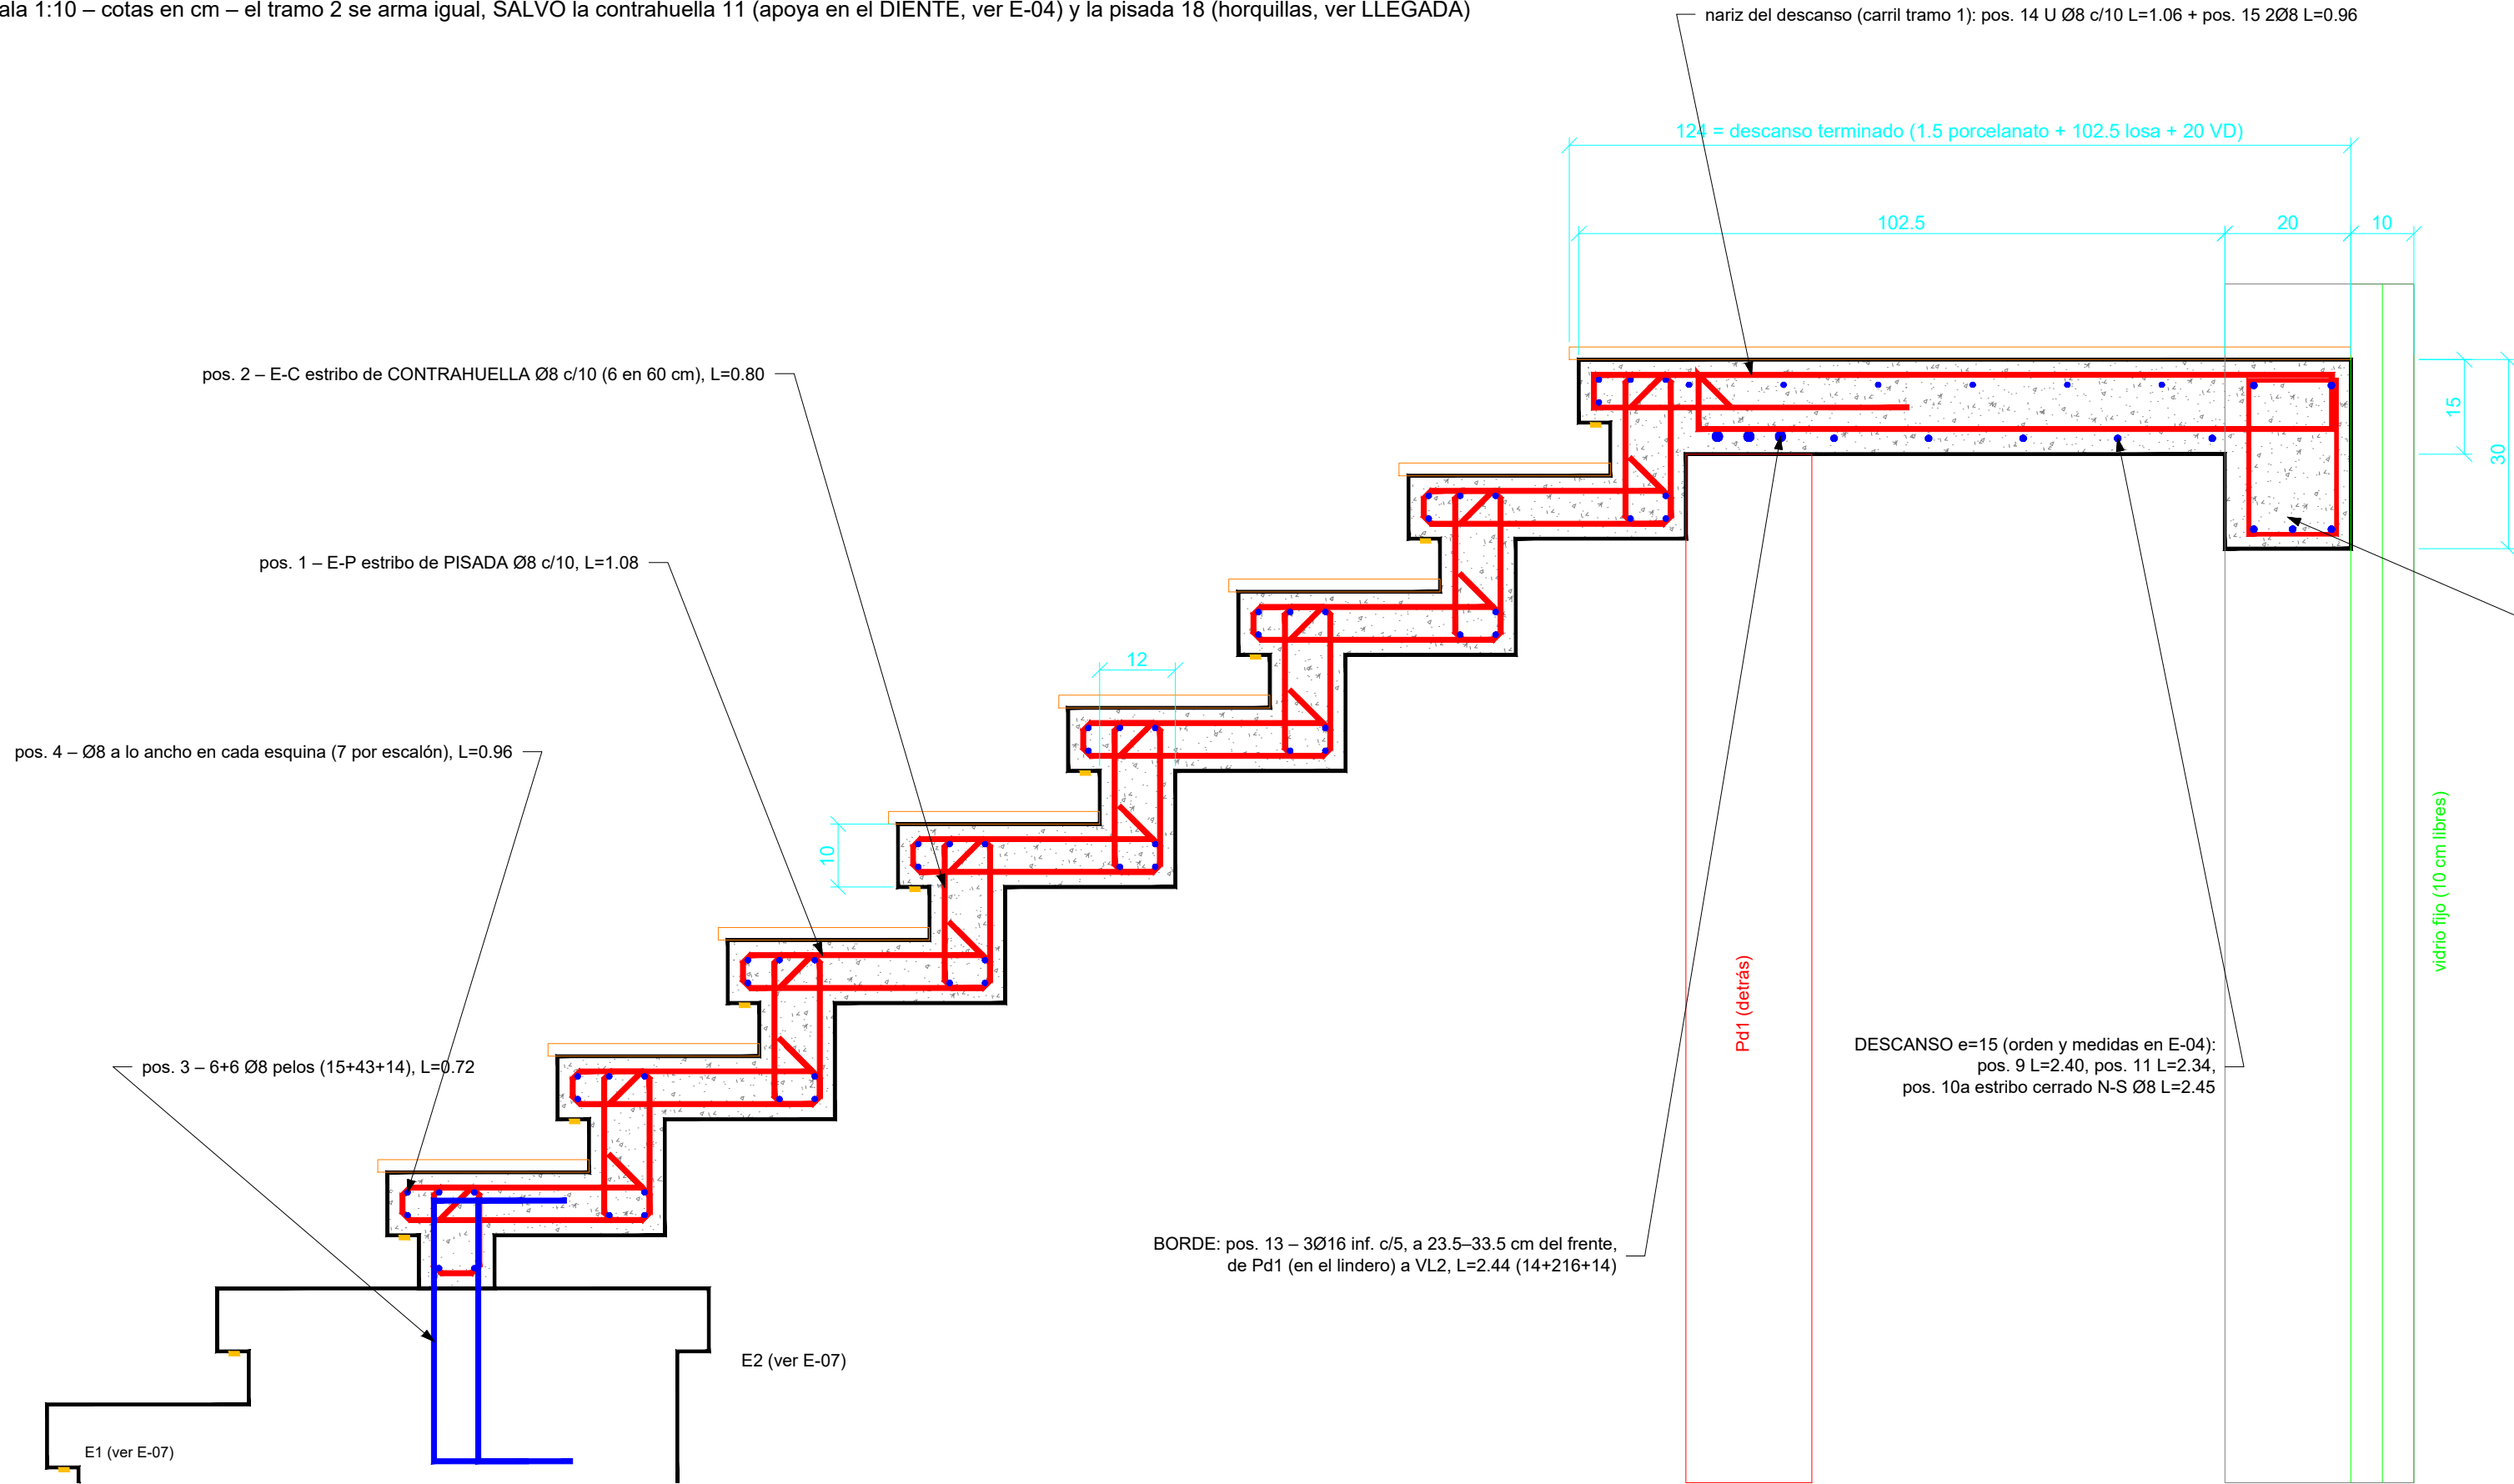


DETALLE PELDAÑO TÍPICO CON LED

Escala 1:5 – medidas en cm

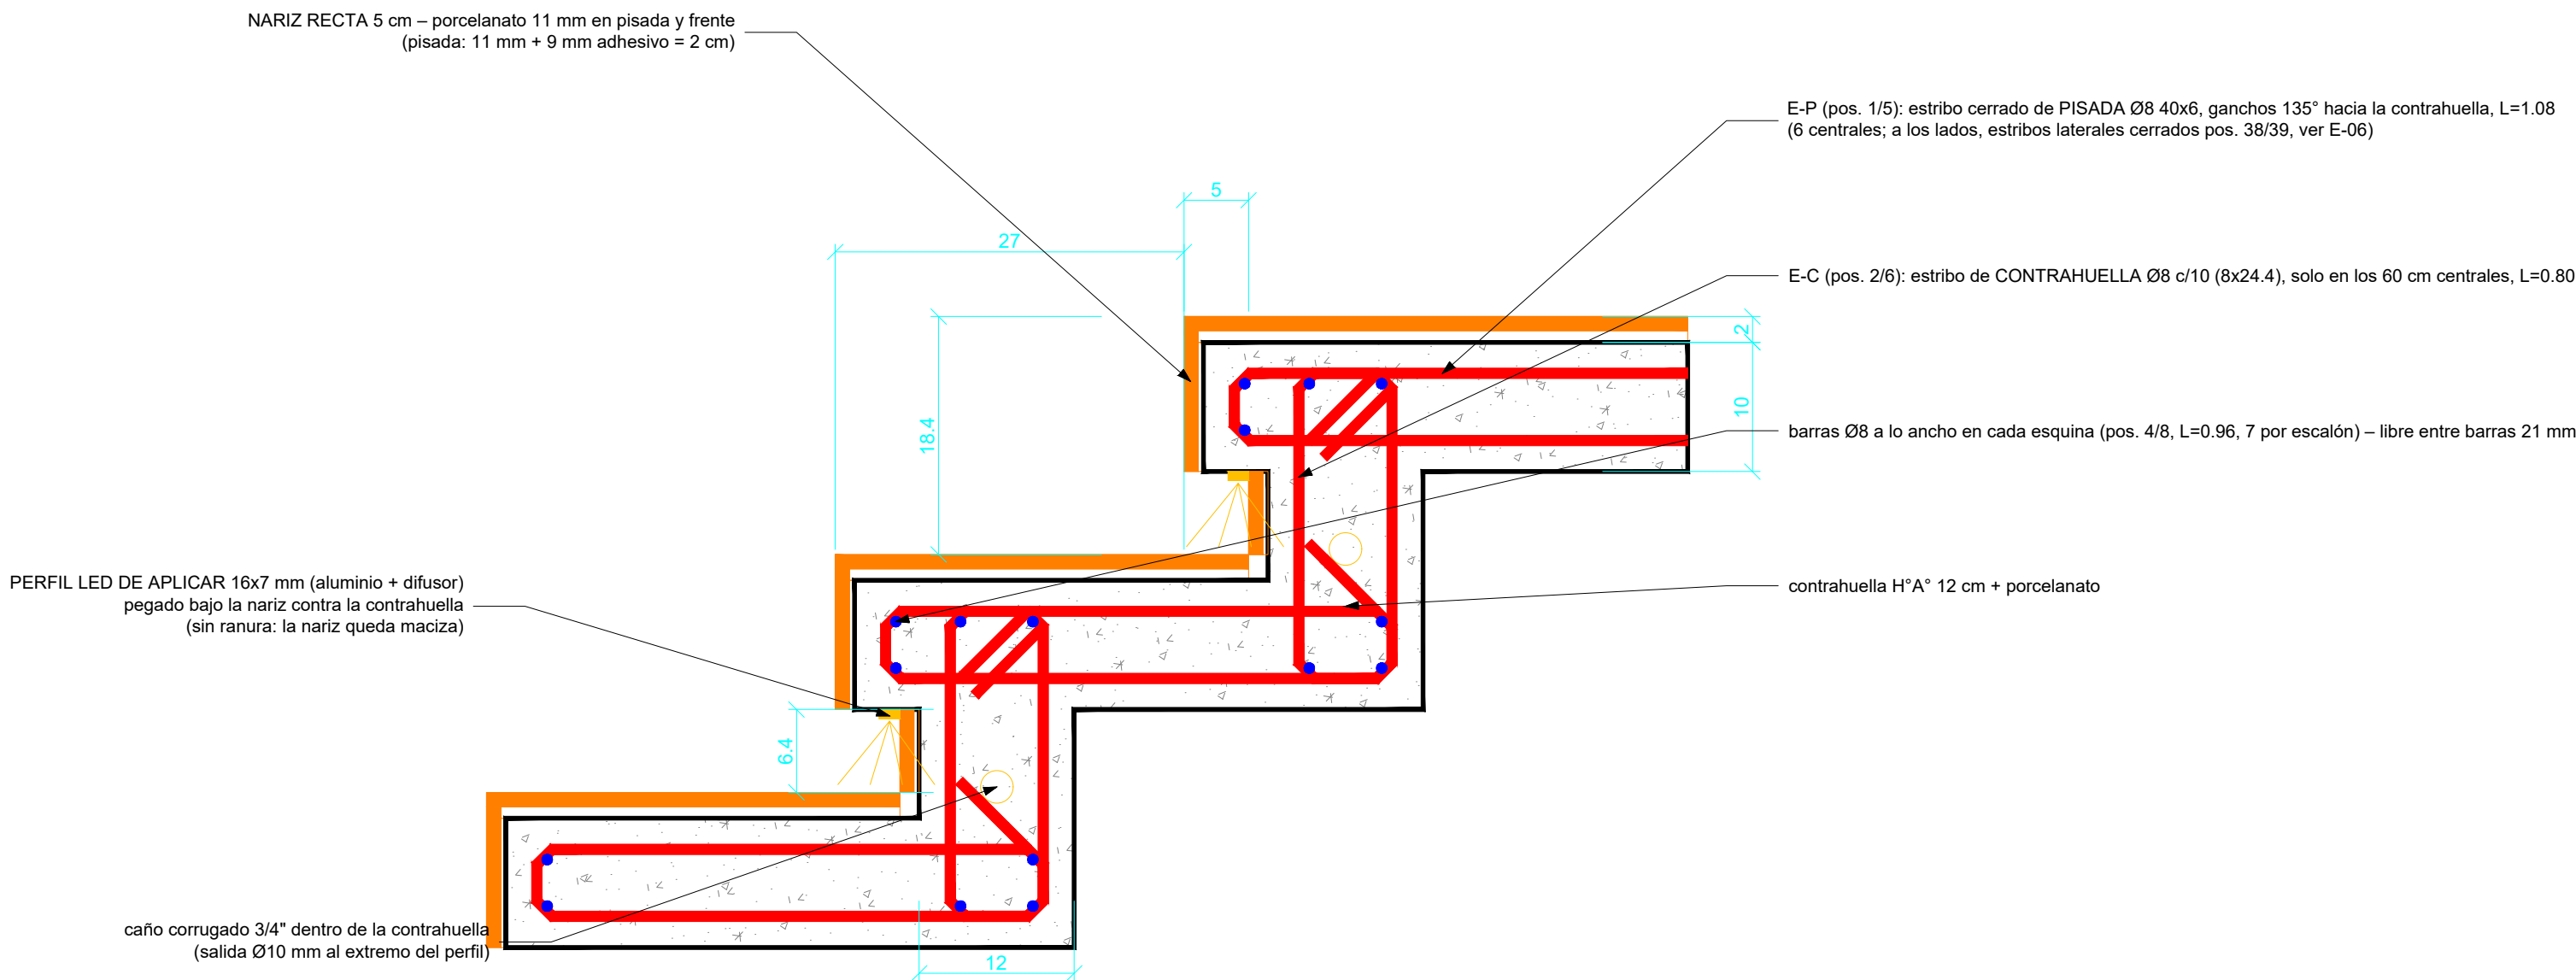


FORMAS DE DOBLADO – TRAMOS

Escala 1:10 – medidas exteriores en cm (descanso en E-04, vigas y Pd1 en E-03, E1 y E2 en E-07)

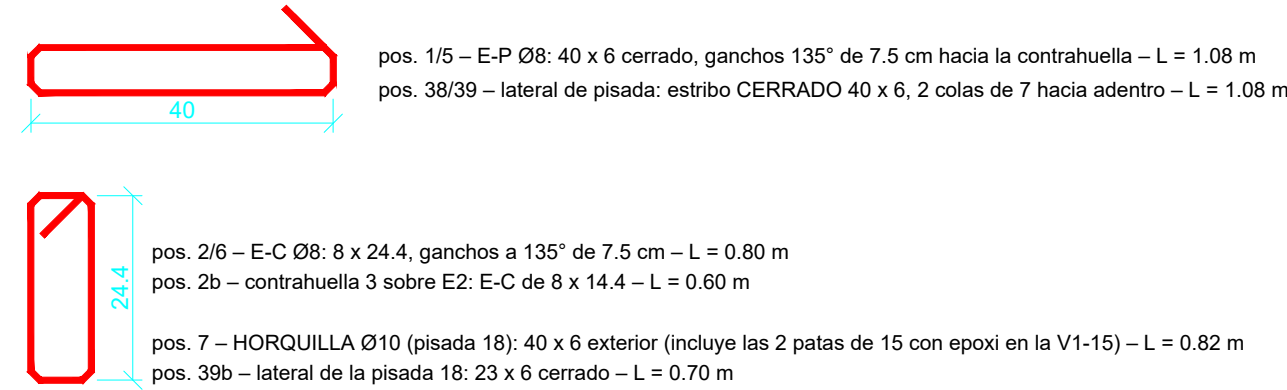


NARIZ – ESPACIOS REALES

Escala 1:2 – medidas en mm

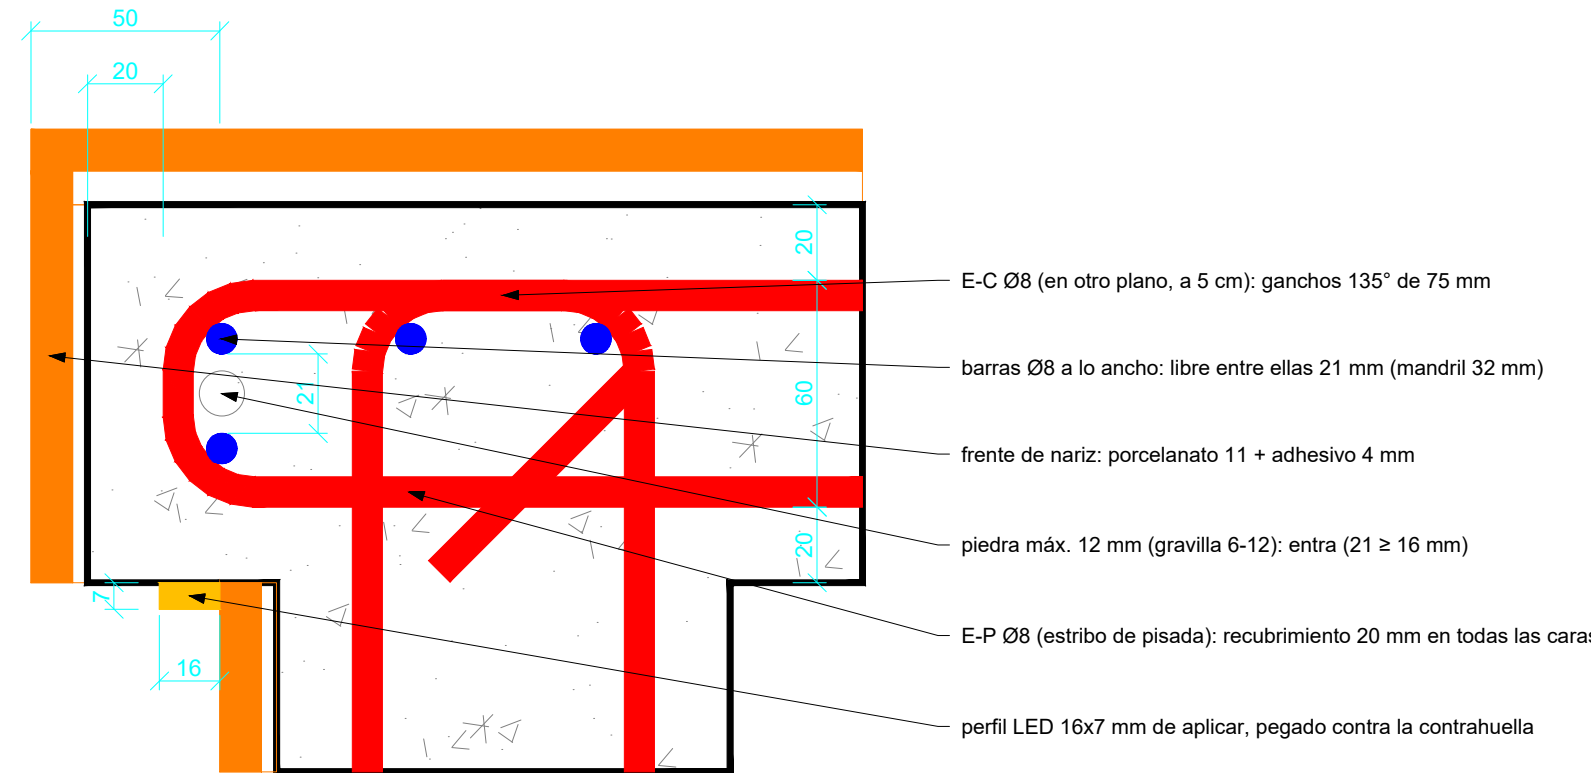

LLEGADA TRAMO 2 A V1-15

Escala 1:10 – horquillas con epoxi en la V1-15

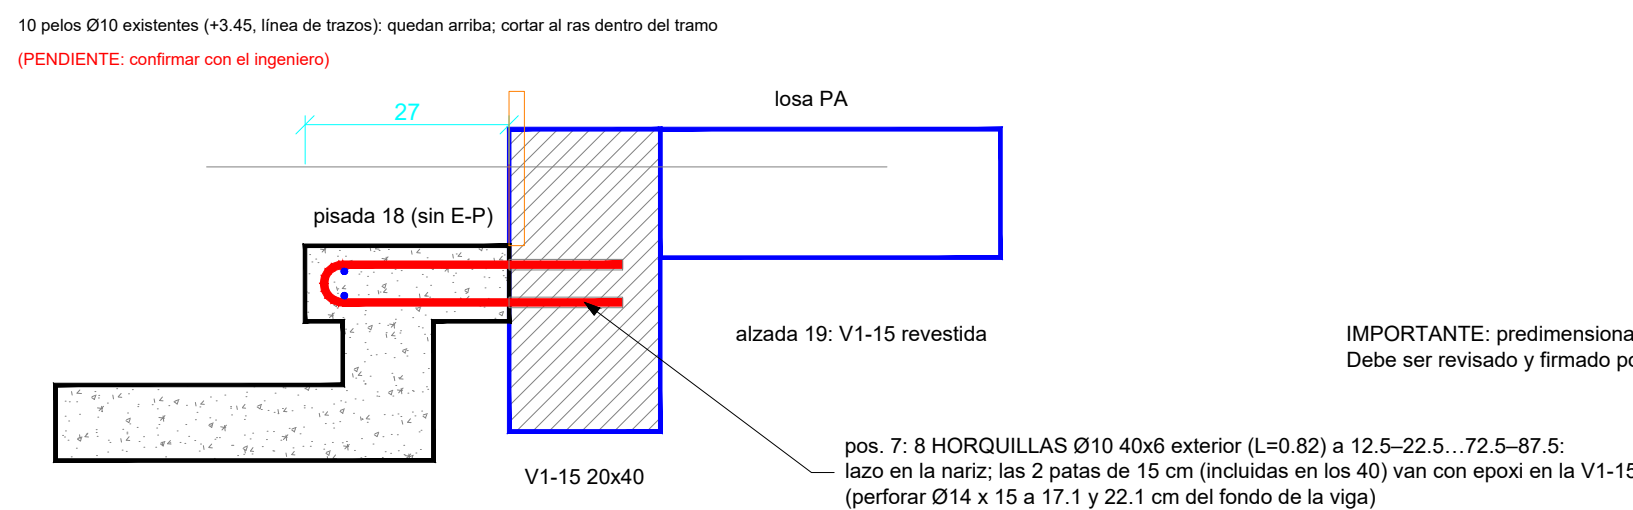

LÁMINAS E-01 a E-08

dónde está cada parte de la escalera

- E-01 Replanteo y SECUENCIA DE OBRA
- E-02 Pilares P18, P19, P20 y nudos
- E-03 Vigas VD, VL1, VL2 y Pd1
- E-04 Descanso
- E-05 Tramos 1 y 2 (esta lámina)
- E-06 Peldaños en planta
- E-07 Arranque E1 y E2
- E-08 Planilla de fierros, hormigón y verificaciones

Recubrimiento 2 cm en todas las caras (medido al estribo). Piedra máx. 12 mm (gravilla 6-12) en tramos y descanso. Espacios reales: ver NARIZ 1:2 (a la derecha).

Huella 27 – alzada 18.4 – 2h + p = 63.8 – franja iluminada bajo la nariz 6.4 cm. Contrahuella solo en los 60 cm centrales (20 cm libres por lado).

OBRA: VIVIENDA RODRIGO RUIZ DÍAZ

ESCALERA SEMI CASCADA EN U – TRAMOS 1 Y 2 – ARMADO

Escala 1:25 (indicada en cada detalle) – Medidas en m (detalles en cm)

Lámina E-05 | Fecha: 01/10/2026 (v21) | H21 – ADN 500

E-05