


ESCALERA – LÁMINA E-06: PLANTA DE ARMADURA DE LOS PELDAÑOS (vista desde arriba)


PLANTA DE ARMADURA – TRAMOS 1 Y 2

Escala 1:10 – cada pisada con sus barras (tramo 1 sube al sur, tramo 2 sube al norte) – rojo E-P / E-C / horquillas, violeta estribo lateral cerrado, azul barras de esquina

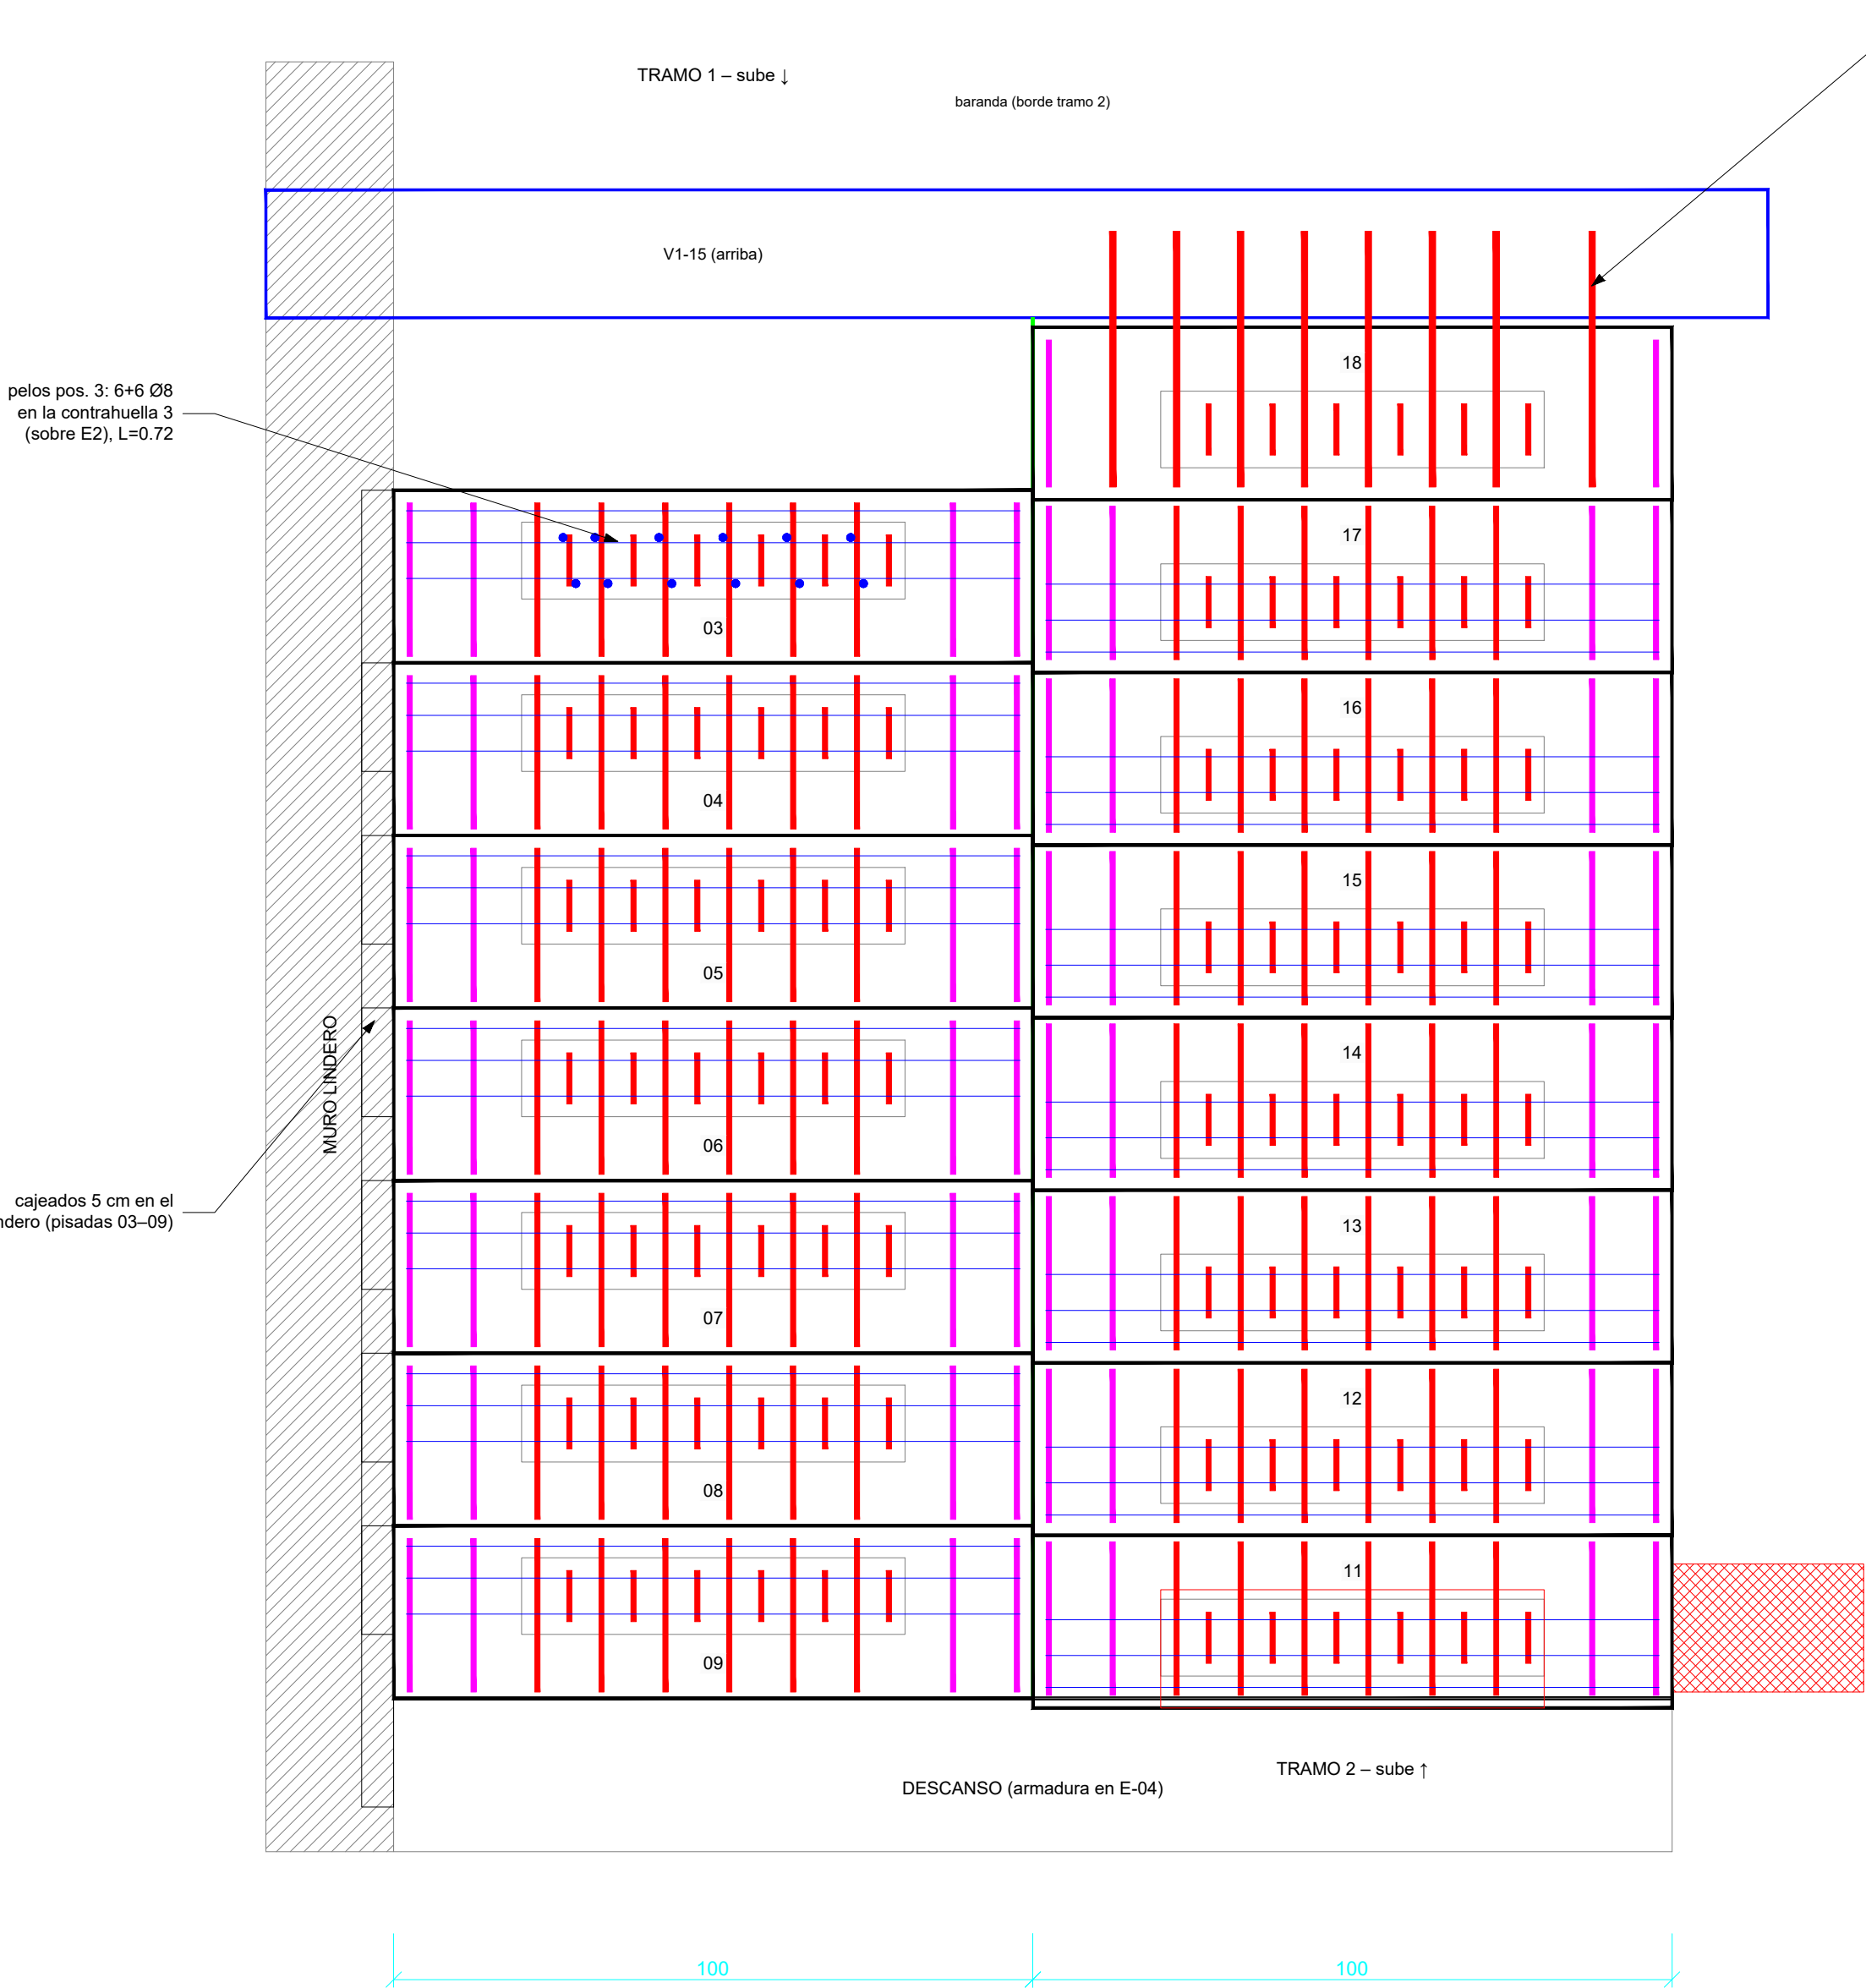


PLANTA DE UN PELDAÑO TIPO

Escala 1:5 – cotas en cm desde el borde OESTE del tramo (lado lindero) y desde la nariz

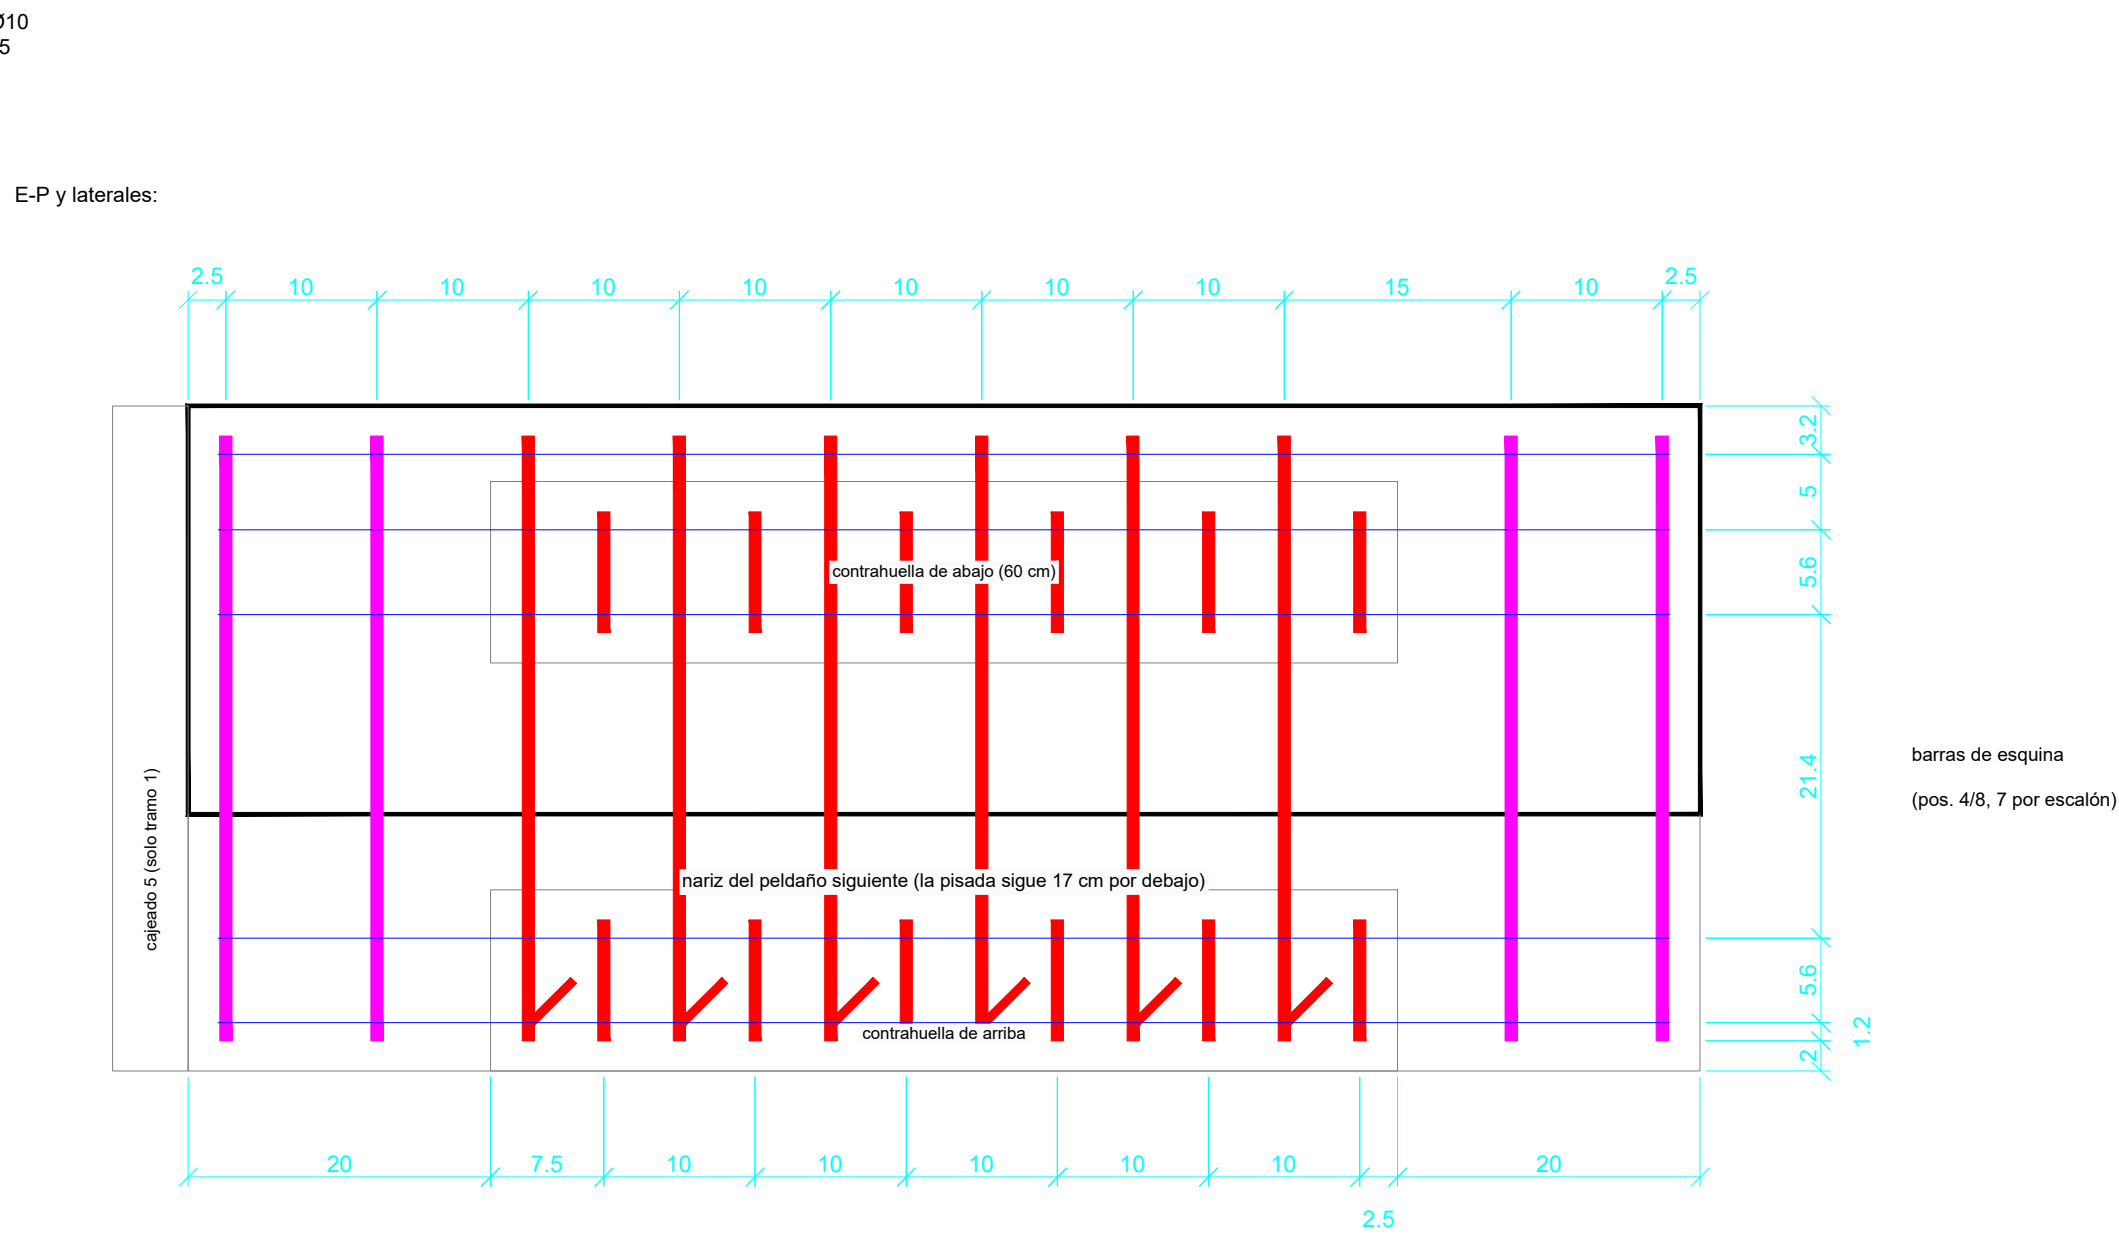

E-C: CORTE TRANSVERSAL POR LA CONTRAHUELLA

Escala 1:5 – corta la pisada k, su contrahuella y el fondo de la pisada k-1

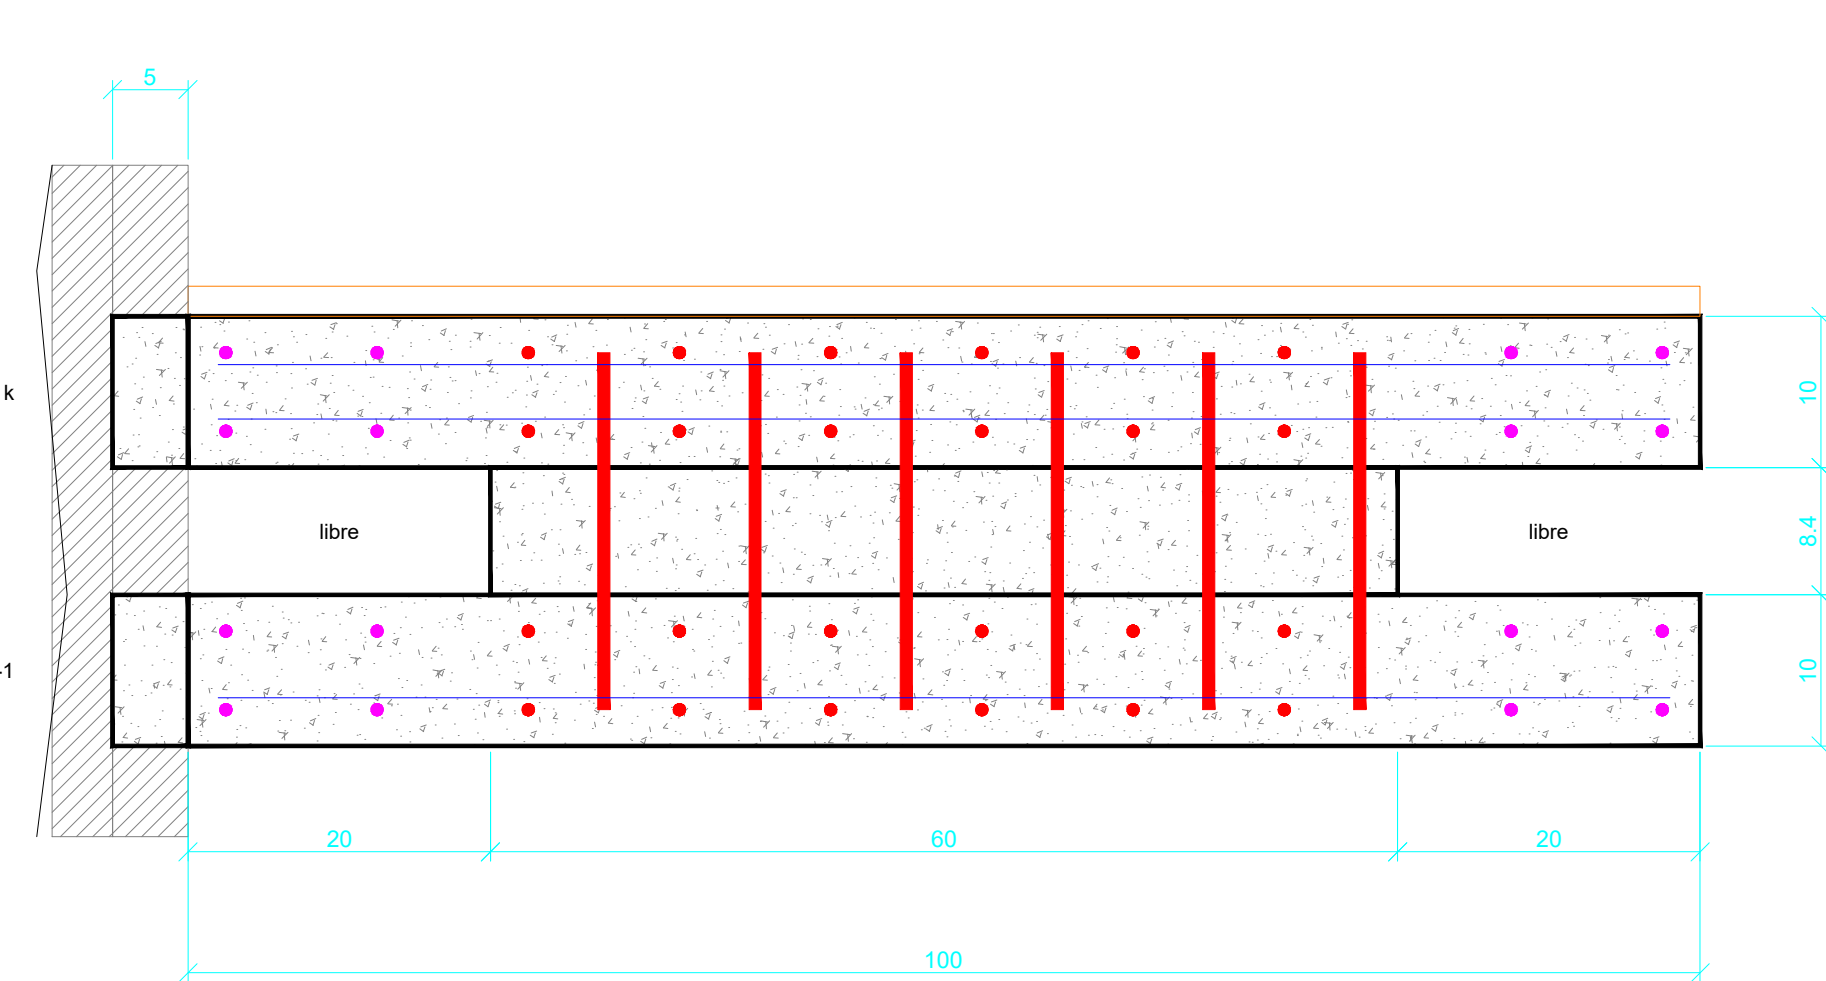

lindero (solo tramo 1): cada pisada entra 5 cm en el muro (cajeado 5x12x45)

POSICIONES A LO ANCHO (cm desde el borde OESTE de cada tramo: tramo 1 = cara del muro lindero; tramo 2 = línea x 1.00)

- E-P cerrado Ø8 40x6 (pos. 1 tramo 1 / pos. 5 tramo 2), 6 por pisada: 22.5 – 32.5 – 42.5 – 52.5 – 62.5 – 72.5. Ganchos 135° hacia la contrahuella de arriba.
- Estribo lateral CERRADO Ø8 40x6 (pos. 38 / 39), 4 por pisada: 2.5 – 12.5 – 87.5 – 97.5. Cierra atrás con 2 colas de 7 cm hacia adentro (L 1.08, igual que el E-P).
- E-C Ø8 8x24.4 (pos. 2 / 6), 6 por contrahuella: 27.5 – 37.5 – 47.5 – 57.5 – 67.5 – 77.5 (5 cm corridos de los E-P). En la contrahuella 03 (sobre E2) son de 8x14.4 (pos. 2b, L 0.60).
- Barras de esquina Ø8 (pos. 4 / 8), 7 por escalón, de 2 a 98 cm (L 0.96), a 3.2 – 8.2 – 13.8 – 35.2 – 40.8 cm de la nariz (las de 3.2 y 40.8 van arriba y abajo).
- Pelos Ø8 (pos. 3, L 0.72 = 15+43+14, entran 27 cm en E2), 6+6 en la contrahuella 3 sobre E2, uno a cada lado del E-P: delanteros 26.5 – 31.5 – 41.5 – 51.5 – 61.5 / traseros 28.5 – 33.5 – 43.5 – 53.5 – 63.5 – 73.5.
- Pisada 18 (sin E-P): 8 horquillas Ø10 (pos. 7) en 12.5 – 22.5 – 32.5 – 42.5 – 52.5 – 62.5 – 72.5 – 87.5, 2 patas de 15 cm con epoxi en la V1-15; laterales 23x6 cerrados (pos. 39b). Si al perforar se toca un estribo de la viga, correr ±2 cm.

ORDEN DE ARMADO DE CADA ESCALÓN

- Colocar los 6 E-C de la contrahuella (27.5 a 77.5).
- Colocar los 6 E-P (22.5 a 72.5) con los ganchos hacia arriba, dentro de la contrahuella siguiente.
- Colocar los 4 estribos laterales cerrados (2.5, 12.5, 87.5, 97.5), con los ganchos hacia adentro.
- Colocar las 7 barras de esquina y atarlas en cada cruce.
- Separadores de 2 cm abajo y a los costados.

IMPORTANTE: predimensionado CIRSOC 201 (H21, ADN 500). Verificar en obra antes de armar. Debe ser revisado y firmado por el profesional responsable de la obra.

OBRA: VIVIENDA RODRIGO RUIZ DÍAZ

ESCALERA SEMI CASCADA EN U – PLANTA DE ARMADURA DE PELDAÑOS

Escala 1:25 (indicada en cada detalle) – Medidas en m (detalles en cm)

Lámina E-06 | Fecha: 01/10/2026 (v21) | H21 – ADN 500

E-06