


ESCALERA – LÁMINA E-05: TRAMOS 1 Y 2 – ARMADO


DETALLE DE ARMADO – TRAMO 1

Escala 1:10 – cotas en cm – el tramo 2 se arma igual, SALVO la contrahuella 11 (apoya directo en el descanso, ver E-04) y la pisada 19 (unida a la losa, ver LLEGADA)

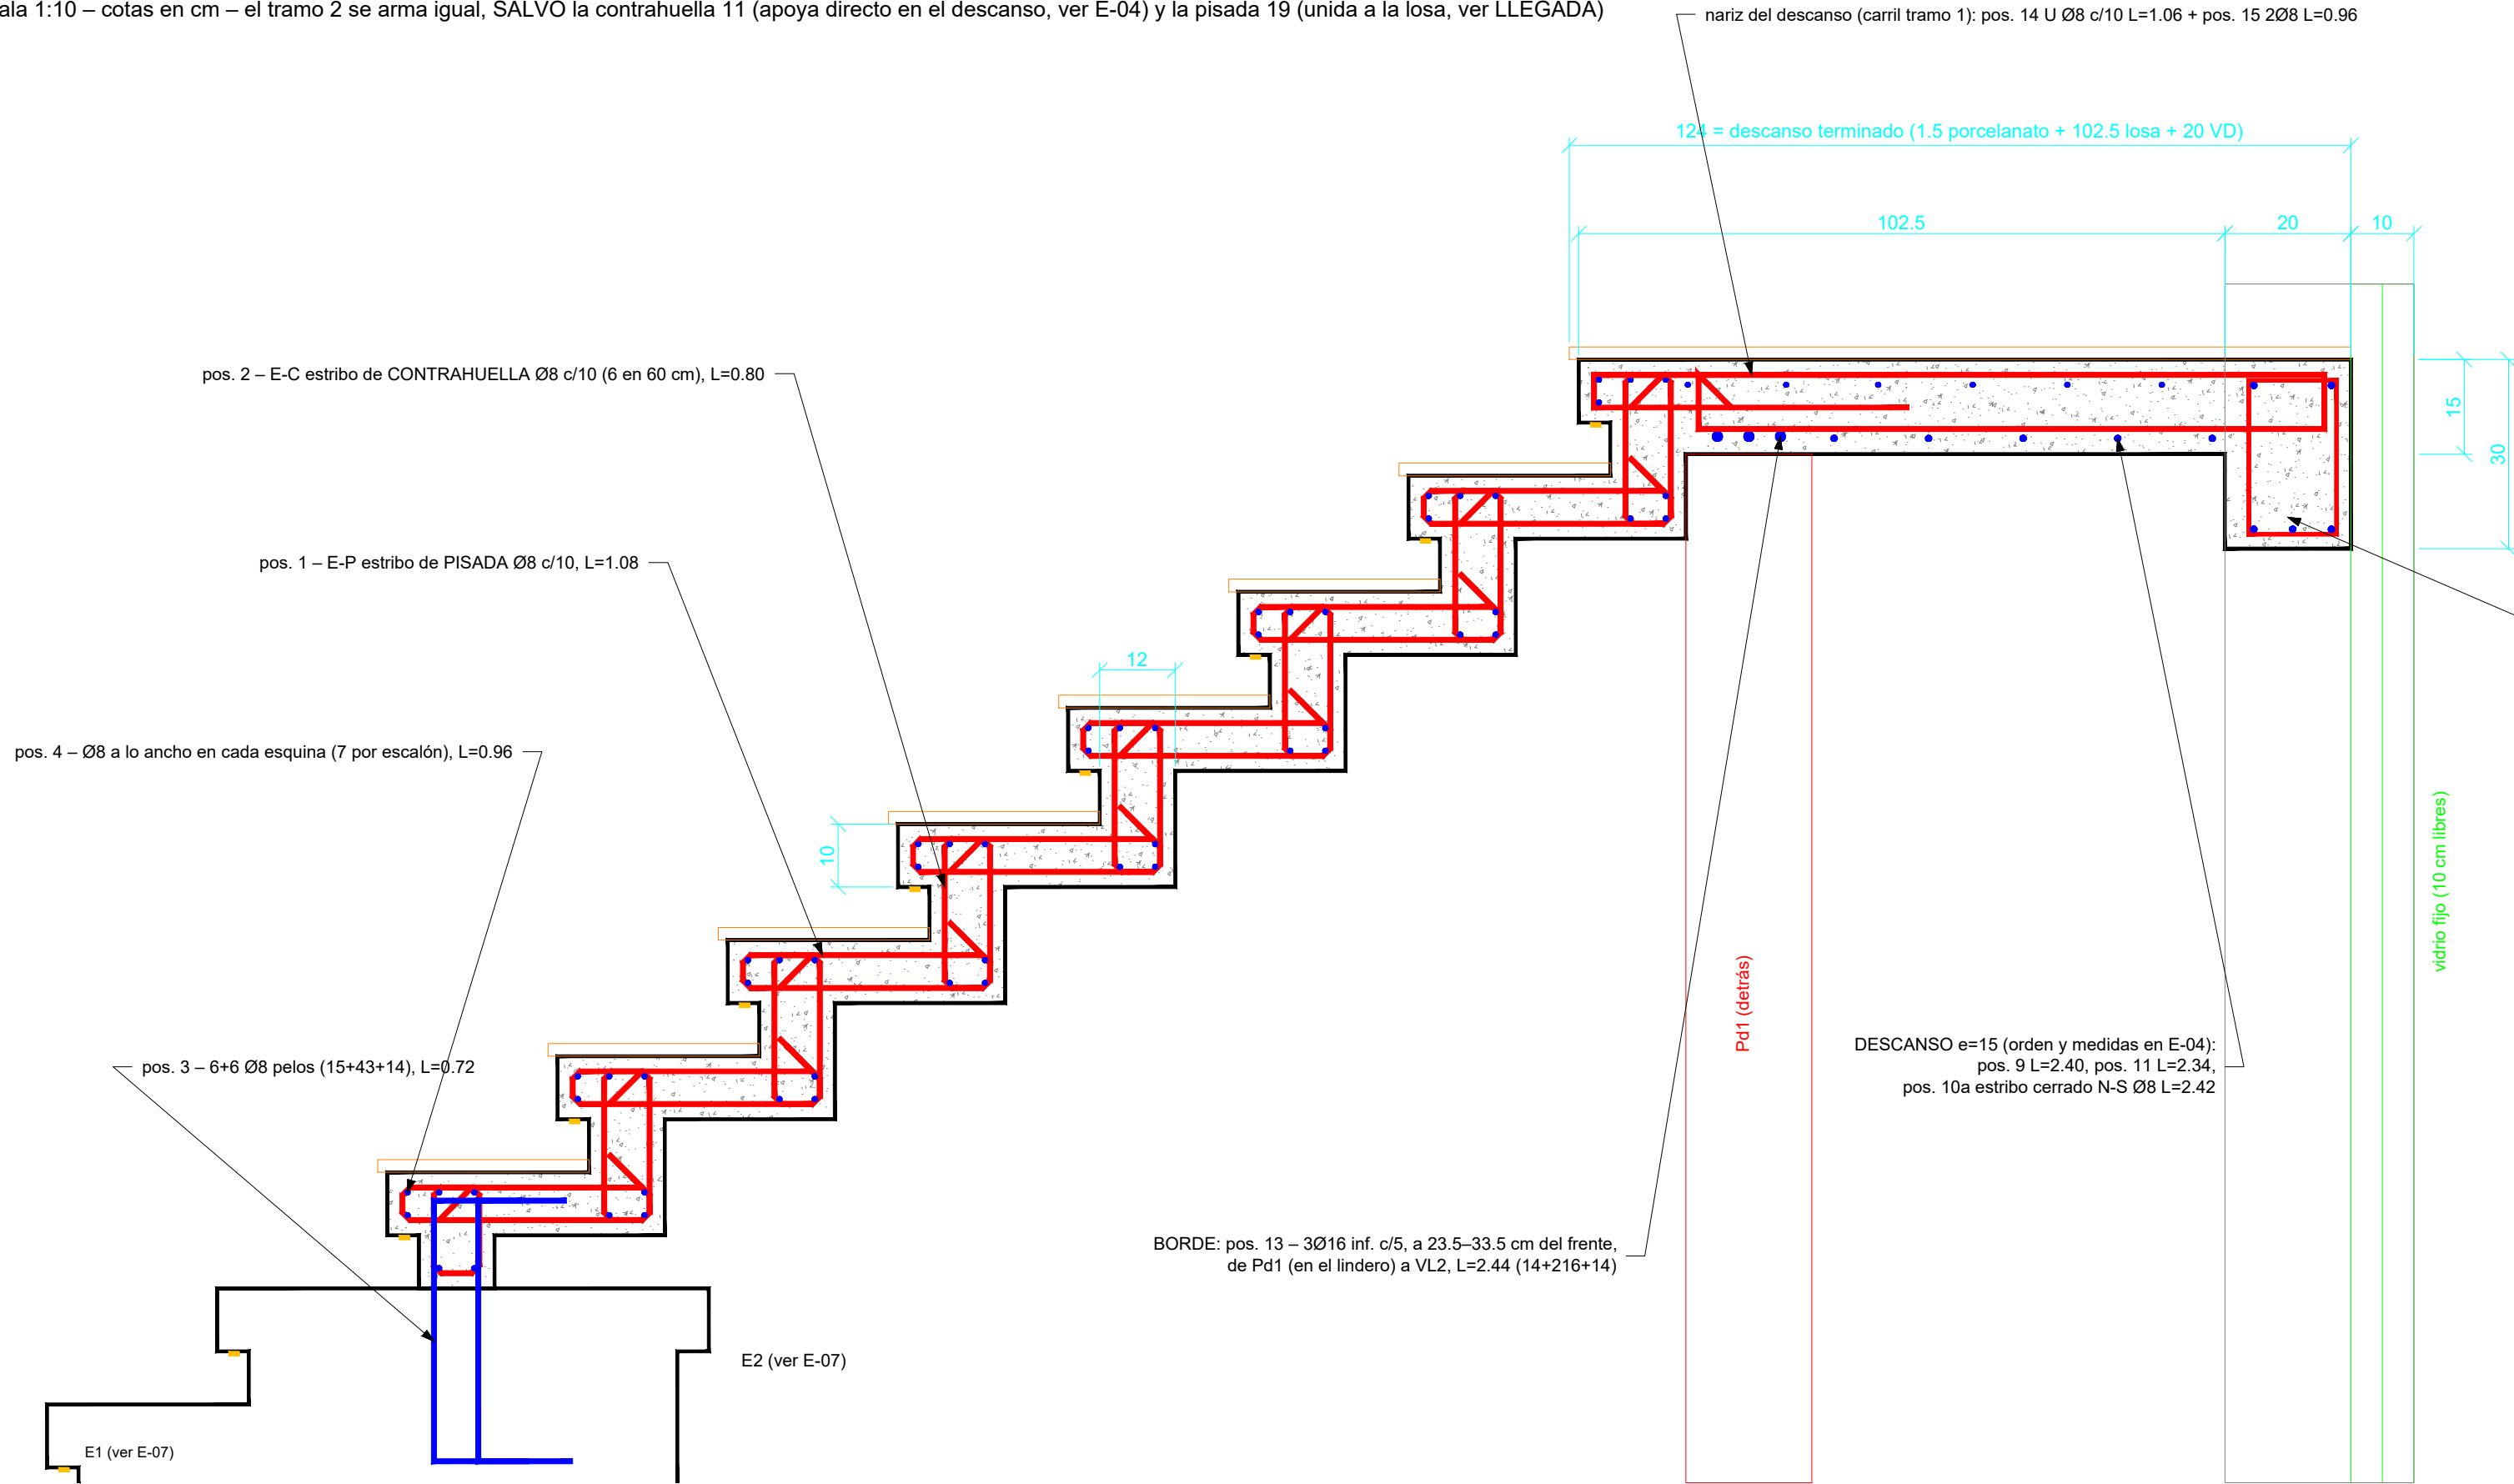

DETALLE PELDAÑO TÍPICO CON LED

Escala 1:5 – medidas en cm

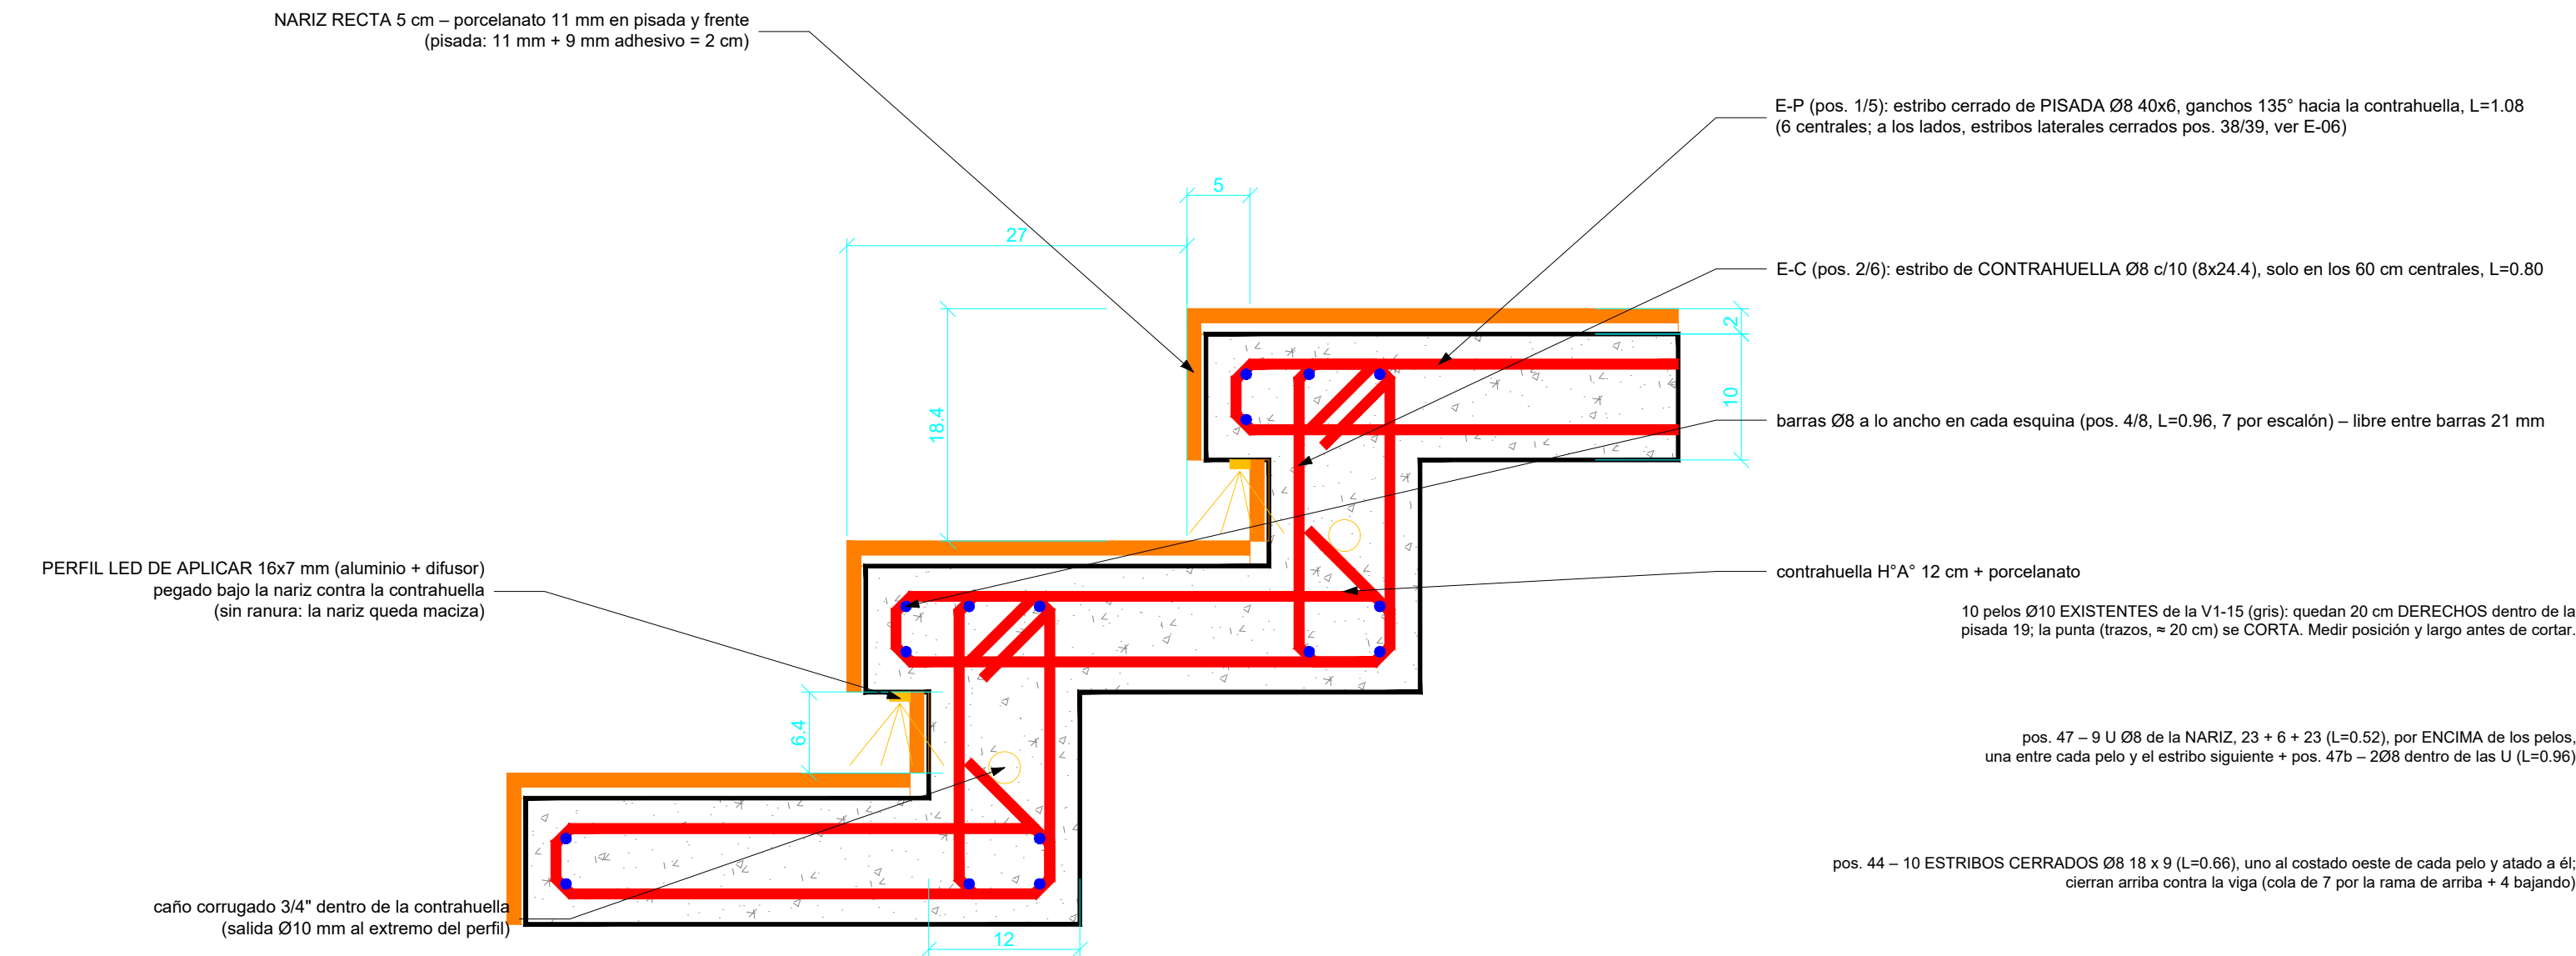


Recubrimiento 2 cm en todas las caras (medido al estribo). Piedra máx. 12 mm (gravilla 6-12) en tramos y descanso. Espacios reales: ver NARIZ 1:2 (a la derecha).

Huella 27 – altura 18.4 – 2h + p = 63.8 – franja iluminada bajo la nariz 6.4 cm. Contrahuella solo en los 60 cm centrales (20 cm libres por lado).


FORMAS DE DOBLADO – TRAMOS

Escala 1:10 – medidas exteriores en cm (descanso en E-04, vigas y Pd1 en E-03, E1 y E2 en E-07)

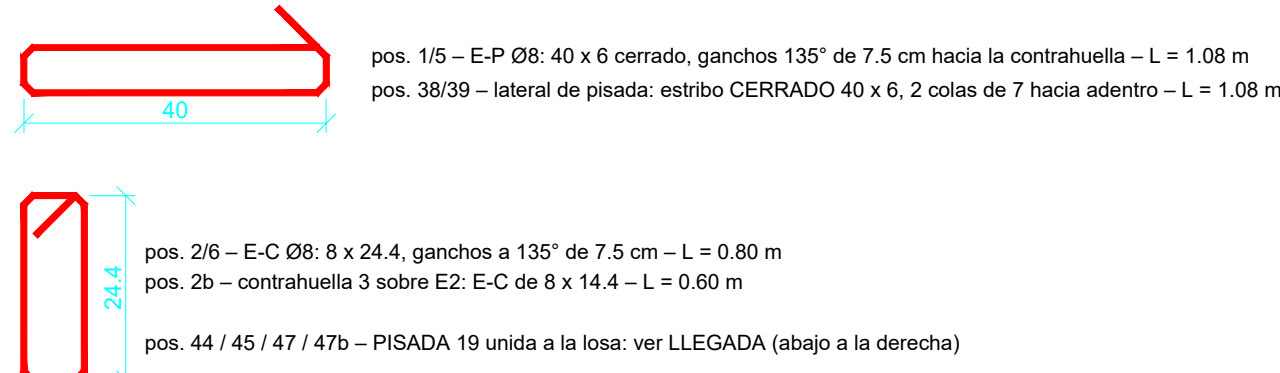


NARIZ – ESPACIOS REALES

Escala 1:2 – medidas en mm

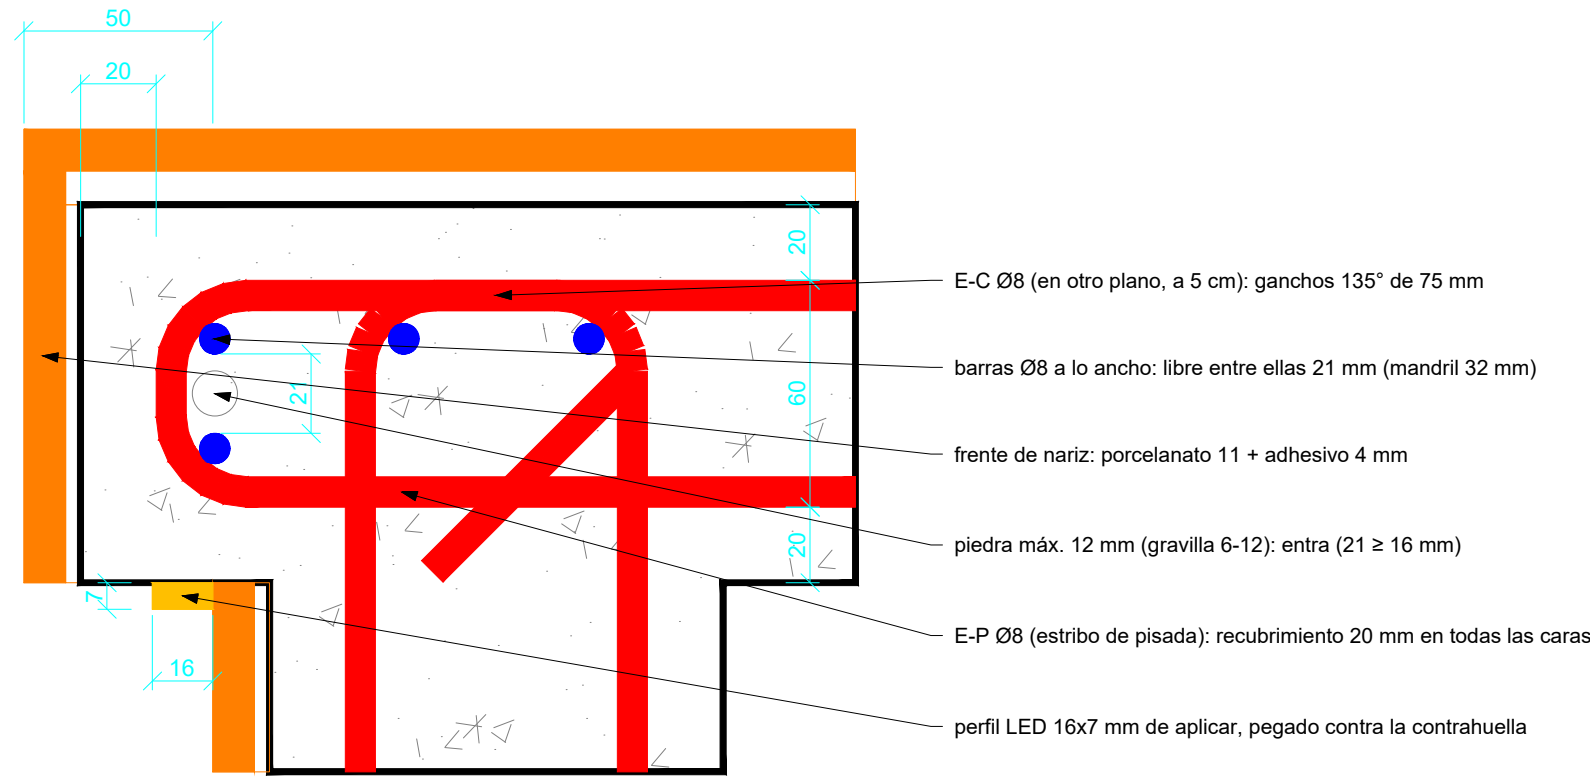

LLEGADA TRAMO 2 – PISADA 19 UNIDA A LA LOSA

Escala 1:5 – cotas en cm – con los 10 pelos Ø10 existentes de la V1-15 (sin epoxi)

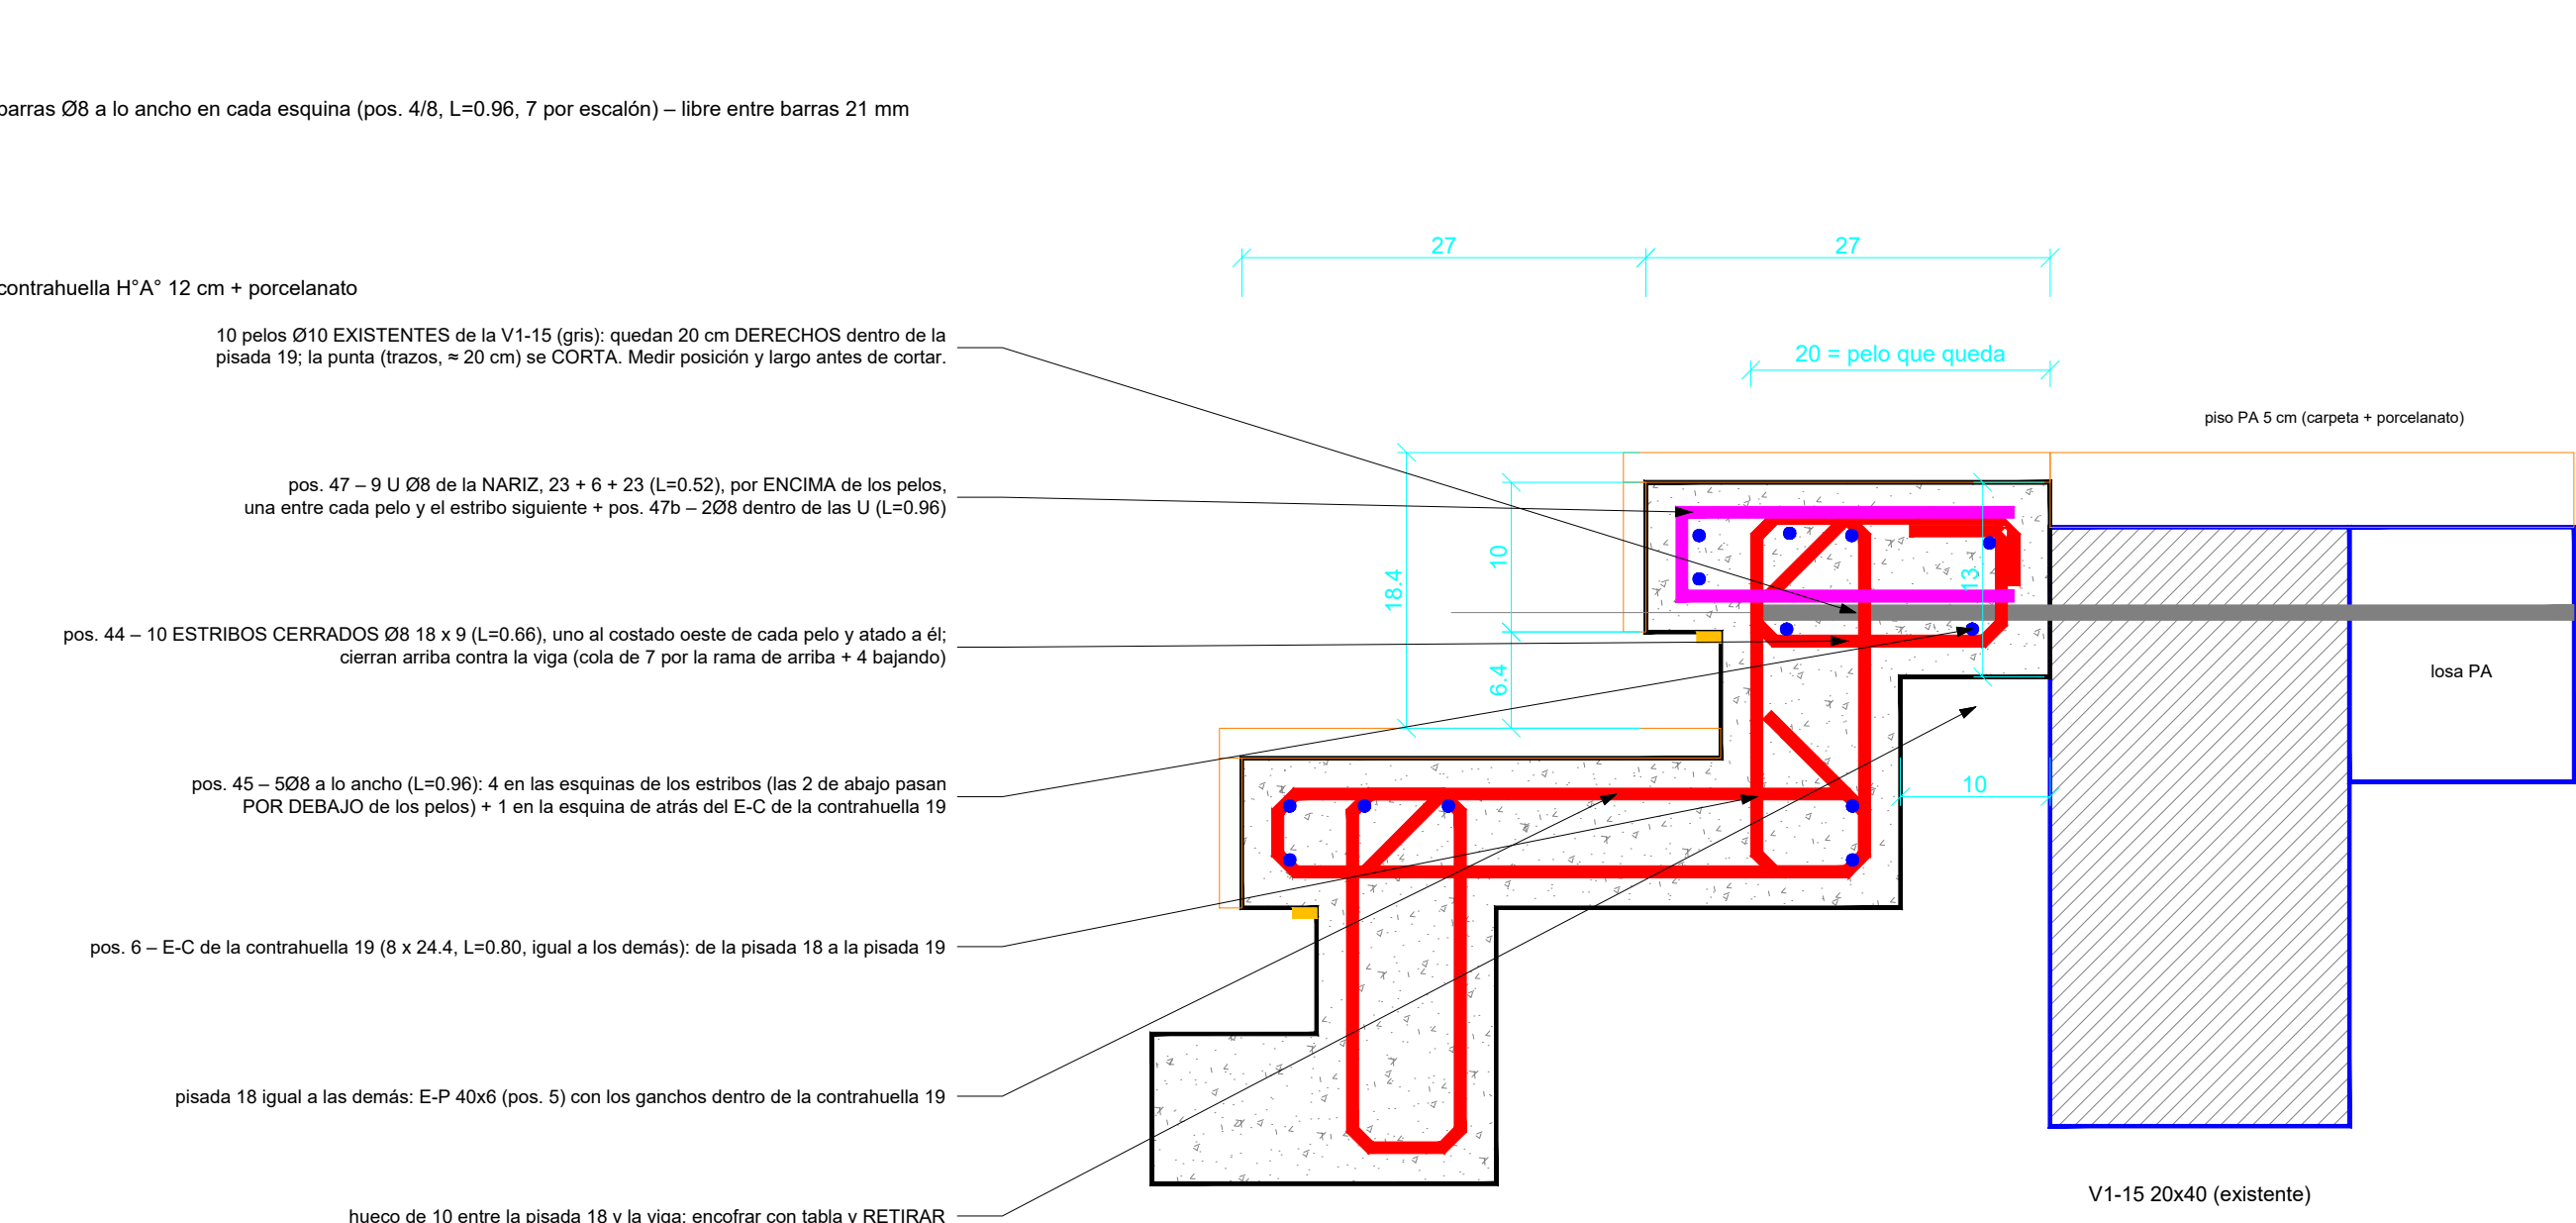

PISADA 19 UNIDA A LA LOSA: nariz de 10 (+3.43 a +3.53) y cuerpo de 13 (+3.40 a +3.53). Hormigón hasta +3.53 + 2 cm de porcelanato = +3.55 (se carpeta de PA llega hasta acá; nivelar con cuidado). Picar y limpiar la cara de la V1-15. Se hormigona junto con el tramo 2 y el descanso; puntales 21 días. Nariz y LED iguales a los demás escalones (12 de nariz vista, 6.4 de LED).

LÁMINAS E-01 a E-08

dónde está cada parte de la escalera

- E-01 Replanteo y SECUENCIA DE OBRA
- E-02 Pilares P18, P19, P20 y nudos
- E-03 Vigas VD, VL1, VL2 y Pd1
- E-04 Descanso
- E-05 Tramos 1 y 2 (esta lámina)
- E-06 Peldaños en planta
- E-07 Arranque E1 y E2
- E-08 Planilla de fierros, hormigón y verificaciones

IMPORTANTE: predimensionado CIRSOC 201 (H21, ADN 500, sobrecarga 3 kN/m²). Debe ser revisado y firmado por el profesional responsable de la obra.

OBRA: VIVIENDA RODRIGO RUIZ DÍAZ

ESCALERA SEMI CASCADA EN U – TRAMOS 1 Y 2 – ARMADO

Escala 1:25 (indicada en cada detalle) – Medidas en m (detalles en cm)

Lámina E-05 | Fecha: 01/10/2026 (v22) | H21 – ADN 500

E-05