


ESCALERA – LÁMINA E-07: ARRANQUE (E1 y E2) – CORTES, PLANTA Y ARMADURA

CORTE A – E1 y E2 (sentido N-S, por el tramo 1)


Escala 1:10 – cotas en cm – el tramo 1 sigue en E-05

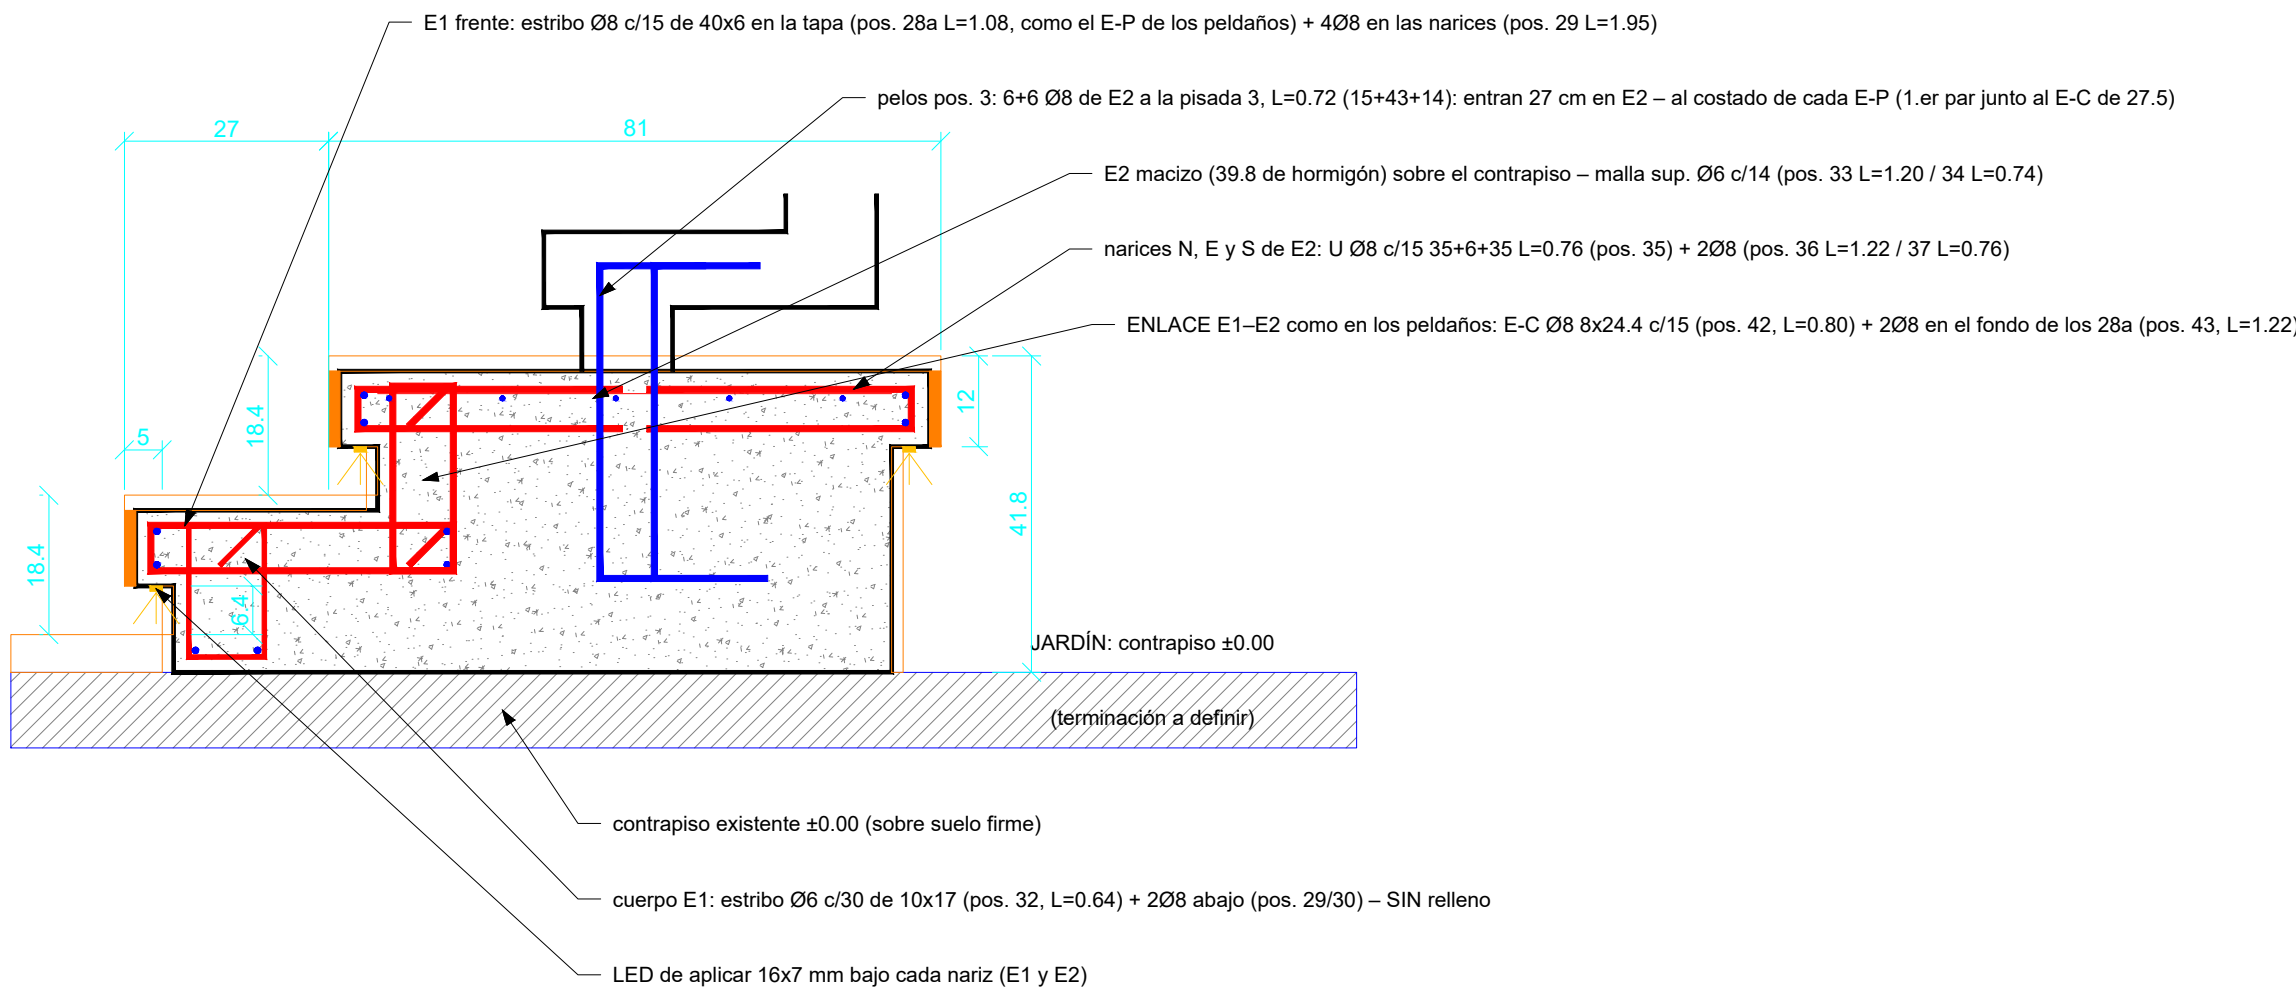

PLANTA E1 y E2

Escala 1:25 – trazo lleno: borde terminado (nariz); trazo cortado: cara del cuerpo (5 cm adentro)

Armadura de E1 y E2 vista desde arriba: ver PLANTA ARMADURA E1 y E2 (a la derecha)

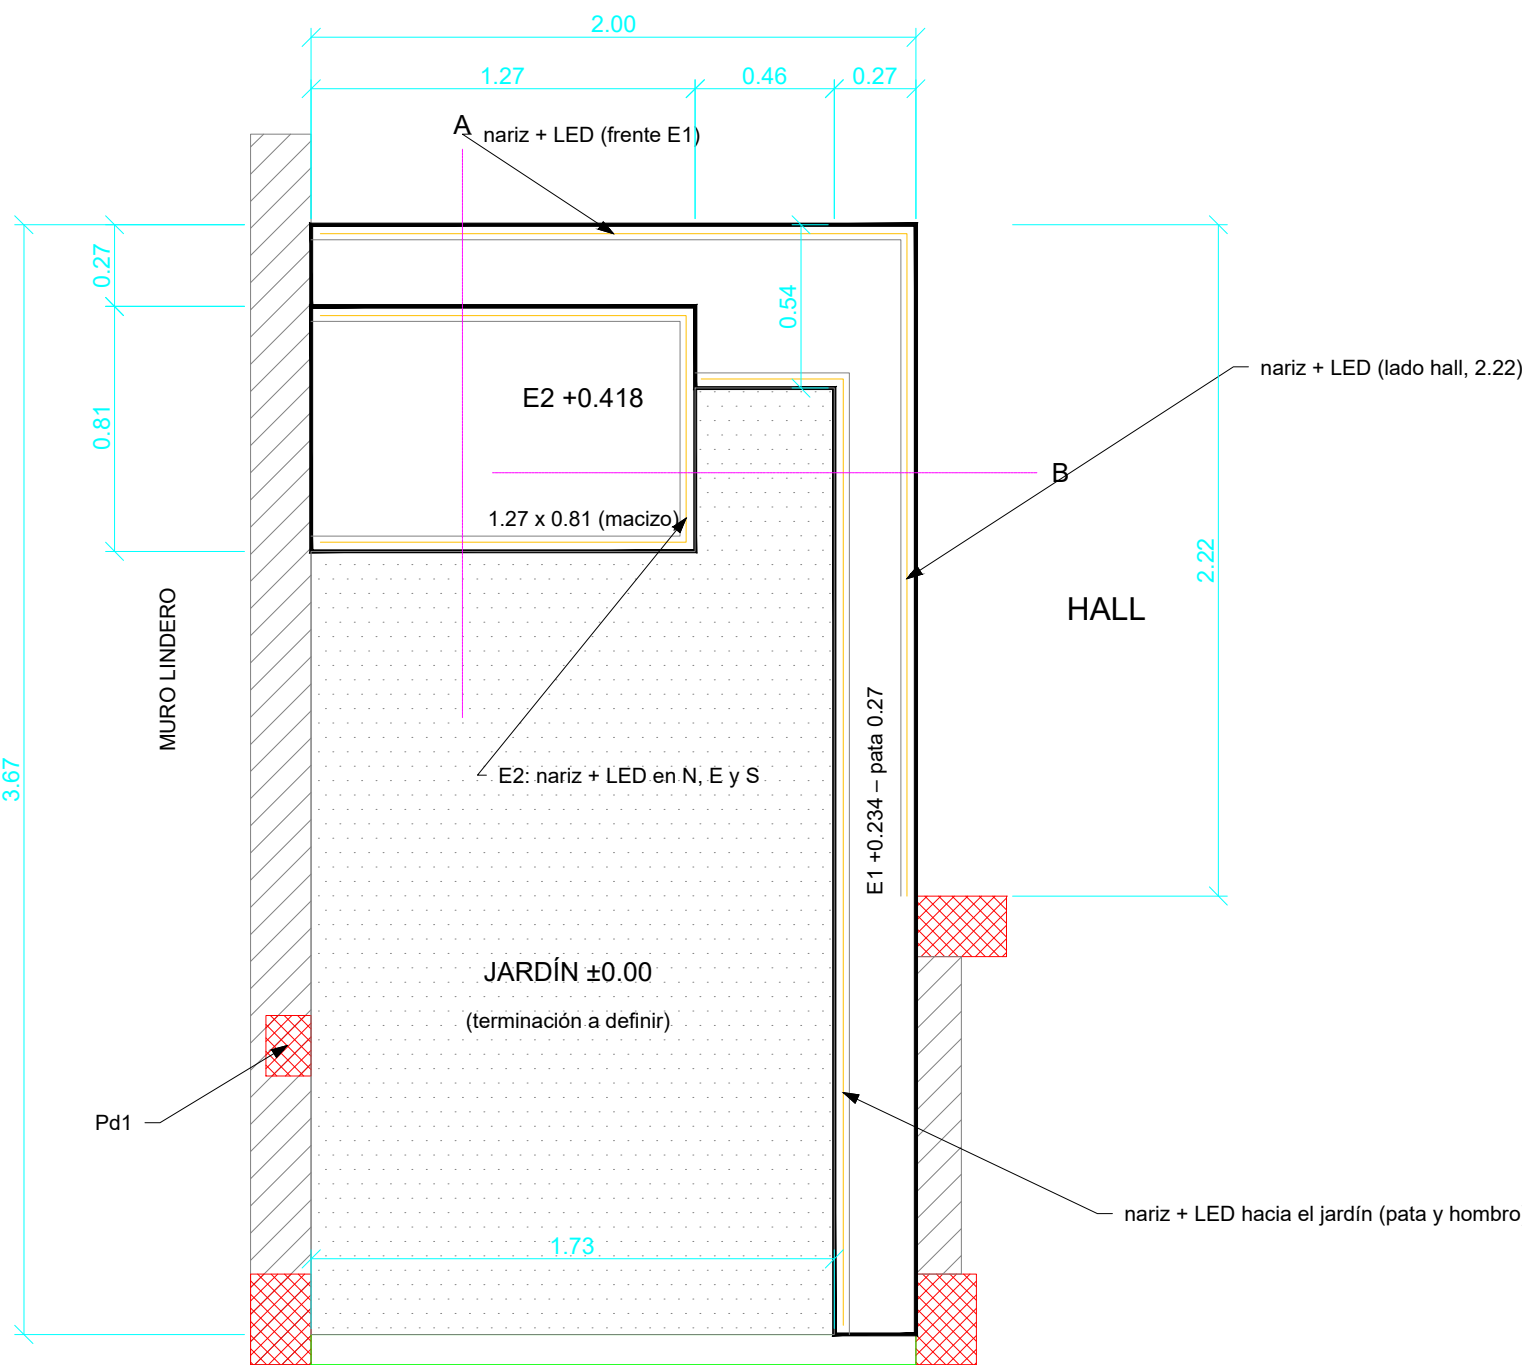


E1 y E2 – CÓMO SE HACEN

- Replantear sobre el contrapiso limpio la L de E1 (frente 2.00 x 0.27 + pata 0.27 junto al hall) y E2 1.27 x 0.81 contra el lindero.
- Dentro de la L queda el JARDÍN en contrapiso ±0.00: sin relleno ni piso (terminación a definir). Dejar caño 3/4" y caja para luces futuras.
- E1 y E2 MACIZOS, en una sola hormigonada: cuerpo retrado 5 cm de cada borde a la vista y tapa de 10 cm que forma la nariz (TODAS las narices iguales a las de los peldaños: 10 cm de hormigón, vuelo 5, porcelanato 1.5 en el canto y LED abajo).
- E1: tapa del frente con estribos Ø8 40x6 c/15 (pos. 28a, como el E-P) que entran bajo E2; pata con 2Ø8 c/15 (toman las 2 narices) + 4Ø8; cuerpo de 14 cm con estribo Ø6 c/30 10x17 + 2Ø8. ENLACE con E2: E-C Ø8 c/15 (pos. 42) + 2Ø8 (pos. 43), como entre dos peldaños.
- E2 (39.8 cm de hormigón): malla sup. Ø6 c/14, narices N, E y S con U Ø8 c/15 + 2Ø8, y los pelos pos. 3 del tramo 1 (entran 27 cm en E2).
- Bajo el tramo 1 no va relleno ni mampostería: apoya en E2 por la contrahuella 3 y vuela 1.80 m hasta el descanso.
- Mezcla A (gravilla 6-12), igual que los tramos: en las narices quedan 21 mm libres entre barras y la piedra 6-18 no pasa. Perfil LED de aplicar bajo cada nariz (también hacia el jardín), caño 3/4" hasta el driver.

PLANTA ARMADURA E1 y E2

Escala 1:20 – vista desde arriba (cortes A y B arriba)

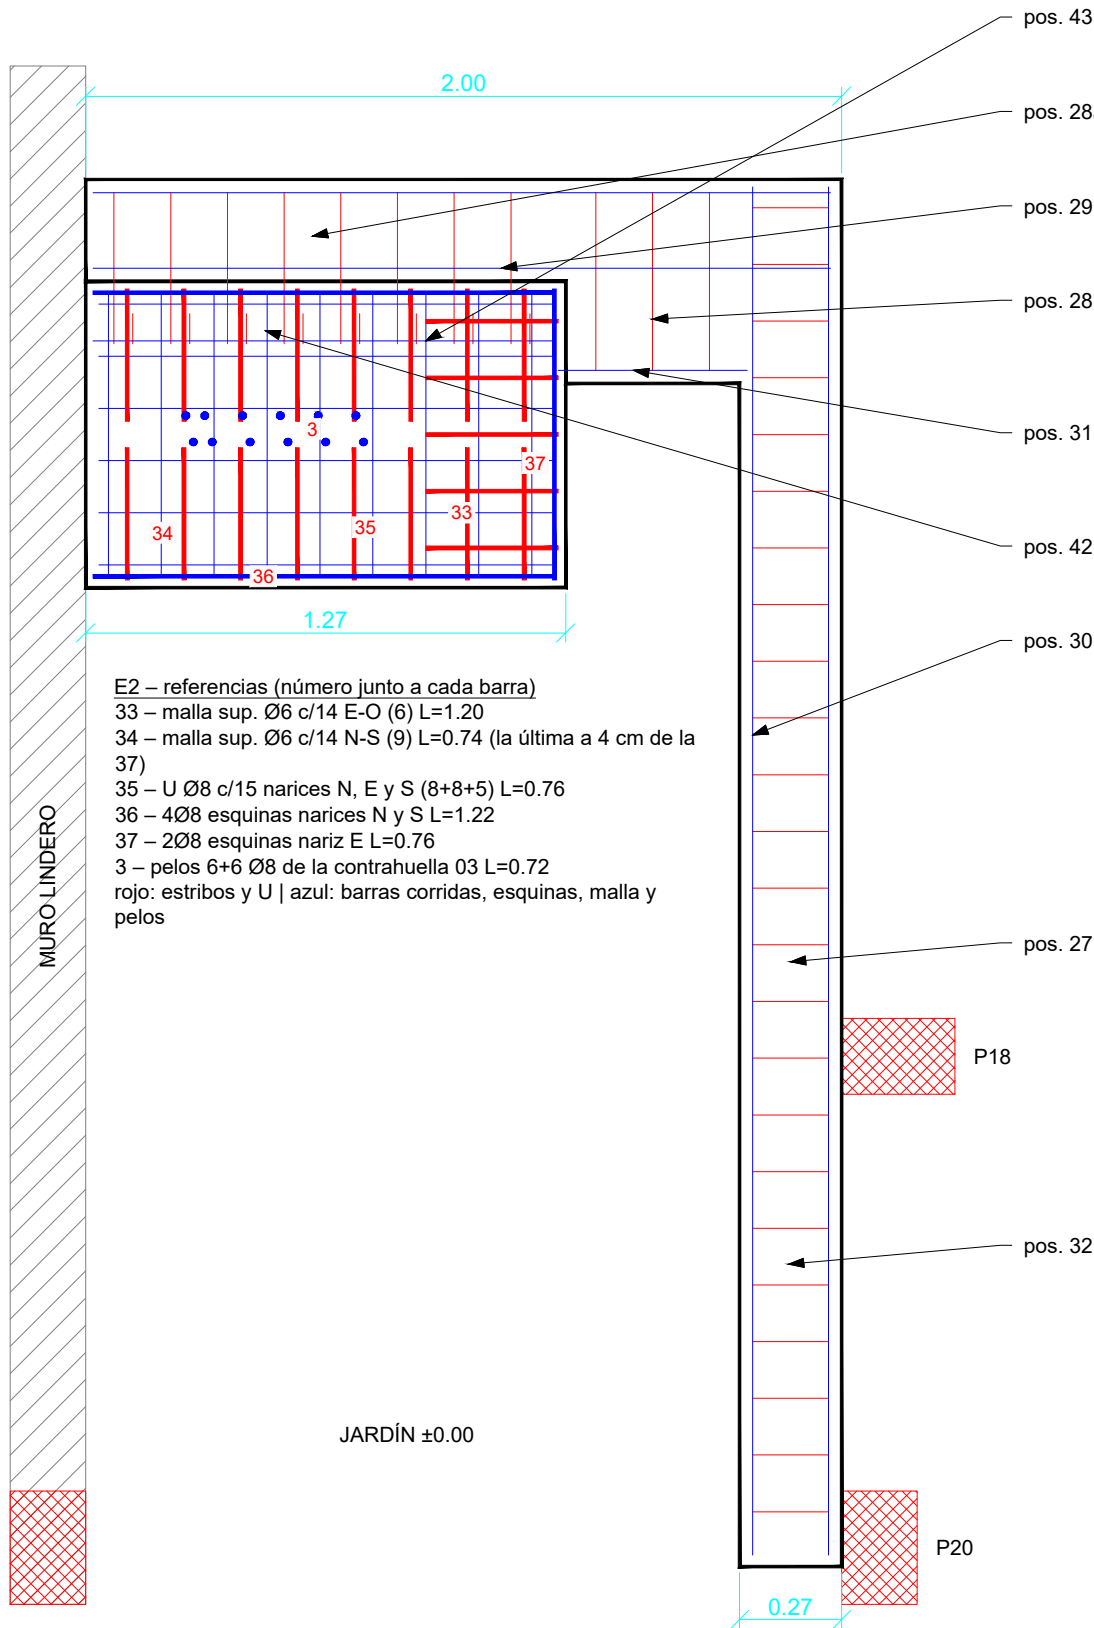

¿HACE FALTA ZAPATA PARA LA ESCALERA?


No hace falta una zapata nueva. Cada apoyo ya tiene fundación:

- Descanso: VD, VL1 y VL2 → pilares P18, P19 y P20 (nuevos, sobre sus bases existentes con pelos).
- Pd1 → viga de fundación del muro lindero (= 17 kN en servicio; verificar esa VF).
- Tramo 2 → descanso y V1-15 (anclajes químicos).
- Tramo 1 abajo → contrahuella 3 → E2 macizo (1.27 x 0.81) → contrapiso → suelo: ≈ 17 kPa, muy por debajo de un suelo compactado (≥ 100 kPa). El suelo bajo el contrapiso fue compactado: E1 y E2 van directo sobre el contrapiso, SIN zapata ni pilotes.

NIVELES: ±0.00 = encadenado · hall +0.05 · E1 +0.234 (21.4 H° + 2 piso) · E2 +0.418 · jardín ±0.00.


CORTE B – pata de E1, jardín y E2 (sentido E-O)

Escala 1:10 – cotas en cm

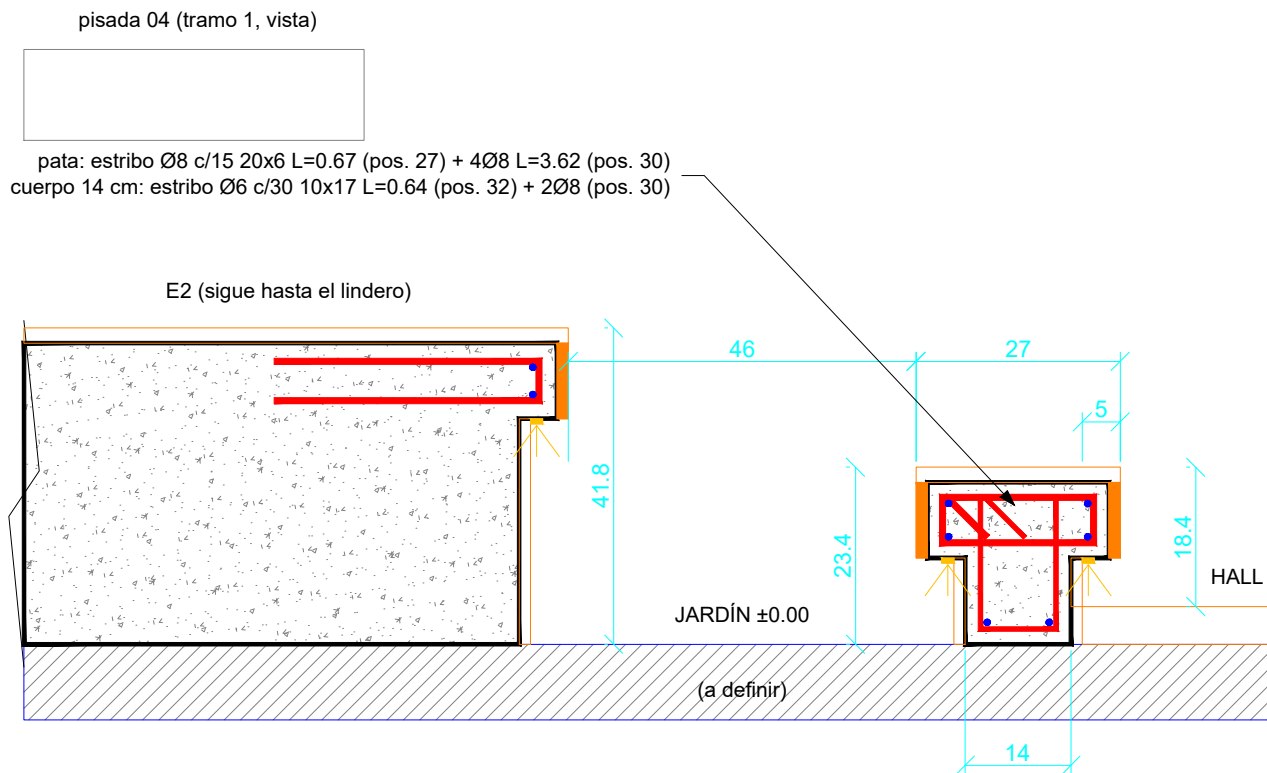

FORMAS DE DOBLADO – E1 y E2

Escala 1:10 (las rectas sin escala) – medidas exteriores en cm

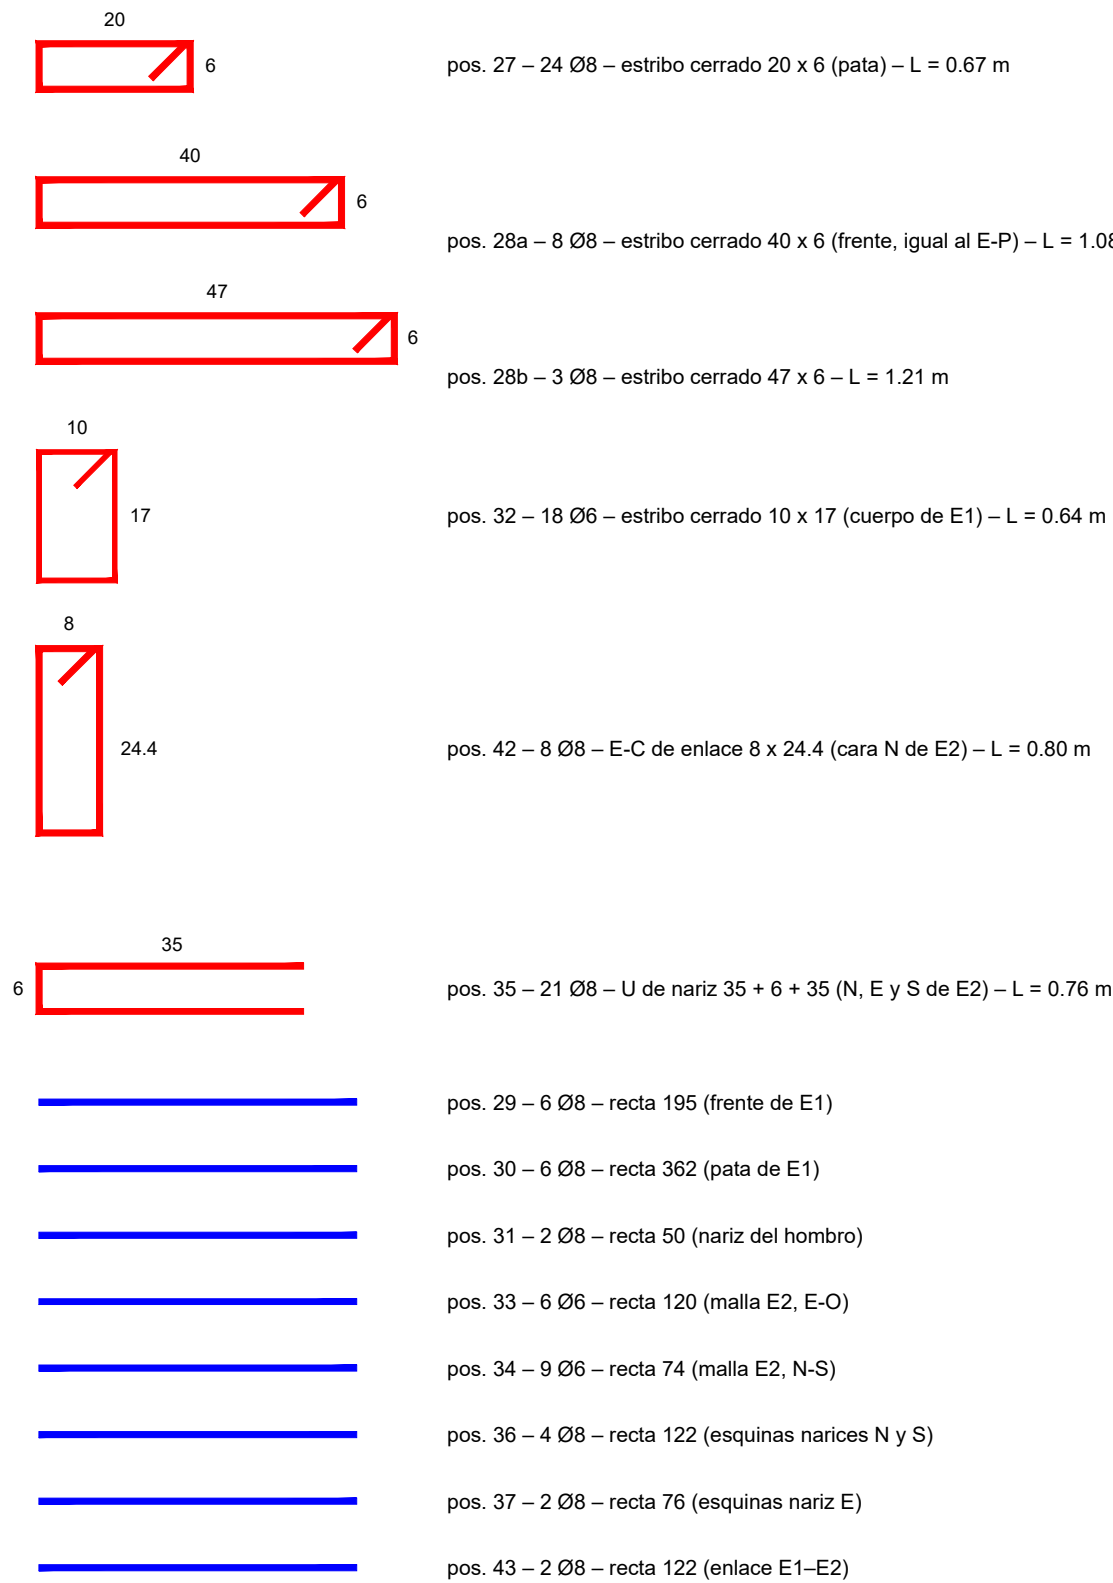

Estribos cerrados: 2 ganchos a 135° de 7.5 cm. Cantidades y kg: planilla general de E-08.

OBRA: VIVIENDA RODRIGO RUIZ DÍAZ

ESCALERA SEMI CASCADA EN U – ARRANQUE E1-E2 Y SU ARMADURA

Escala 1:25 (indicada en cada detalle) – Medidas en m (detalles en cm)

Lámina E-07 | Fecha: 01/10/2026 (v22) | H21 – ADN 500

E-07